


1 CROQUI DE SITUAÇÃO
SEM ESCALA

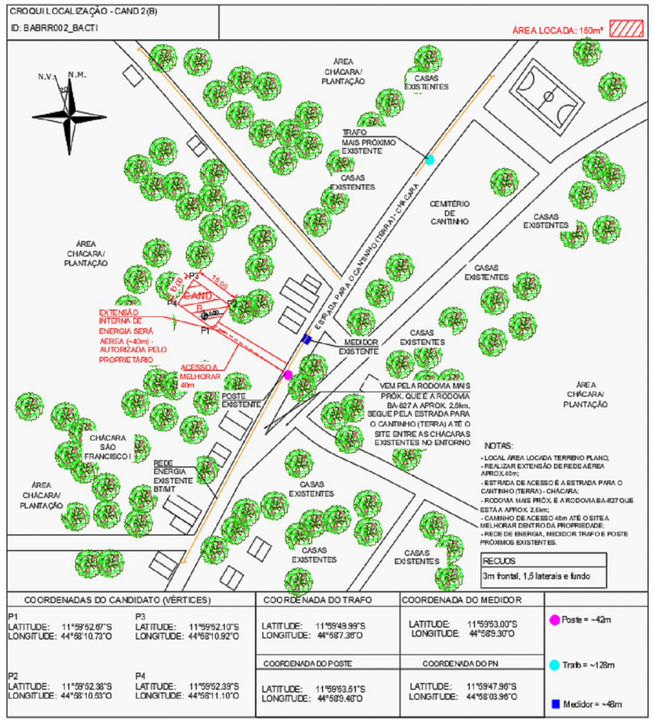

2 LOCALIZAÇÃO – FONTE GOOGLE EARTH
SEM ESCALA

A entrega a terceiros e a reprodução deste documento, assim como o uso e a revelação do seu conteúdo, são proibidos, salvo por autorização expressa. Os infratores respondem por perdas e danos. No caso do concessão de patentes de invenção, modelos de utilidade, modelos ou desenhos industriais, ficam reservados os direitos de exclusividade

Pena	Esp.	Cor
1	0,15	7
2	0,25	7
3	0,20	7
4	0,15	7
5	0,40	7
6	0,50	7
7	0,20	7
8	0,15	7
9	0,10	7
10	0,15	1
20	0,15	1
30	0,20	7
80	0,15	3
98	0,20	98
142	0,15	142
170	0,15	5
210	0,15	6

ESCALA PLOT : 1/100
FORMATO ABNT A3 297x420


FORMATO A3 (420x297mm)

OBSERVAÇÕES:

COMENTÁRIO DE REVISÕES

REV.	DATA	DESCRIÇÃO	DESENHO	VERIFICAÇÃO
02	27/03/2026	COMPATIBILIZADO COM FUNDAÇÃO	FERA	WINITY
01	25/03/2026	ALTURA DAS ANTENAS	FERA	WINITY
00	16/03/2026	EMISSÃO INICIAL	FERA	WINITY


SOLICITANTE: vivo
CONCERSSIONÁRIA:
ENDEREÇO: **POVOADO CANTINHO DO SENHOR DOS AFLITOS, N°27 - BARREIRAS/BA - CEP: 47.809-999**
DETENTORA: winity TELECOM
COORDENADAS: **LAT.: 11°59'52.59"S LONG.: 44°58'10.46"W**
REVISÃO: 02
RESP. TÉC. EXECUÇÃO: F.E.R.A. PROJETOS E ENGENHARIA
PROJETO EXECUTIVO
SITE: BABRR002_C BACTI
EMISSÃO: 16/03/2026
ASSUNTO: IMPLANTAÇÃO
FOLHA: 01/15

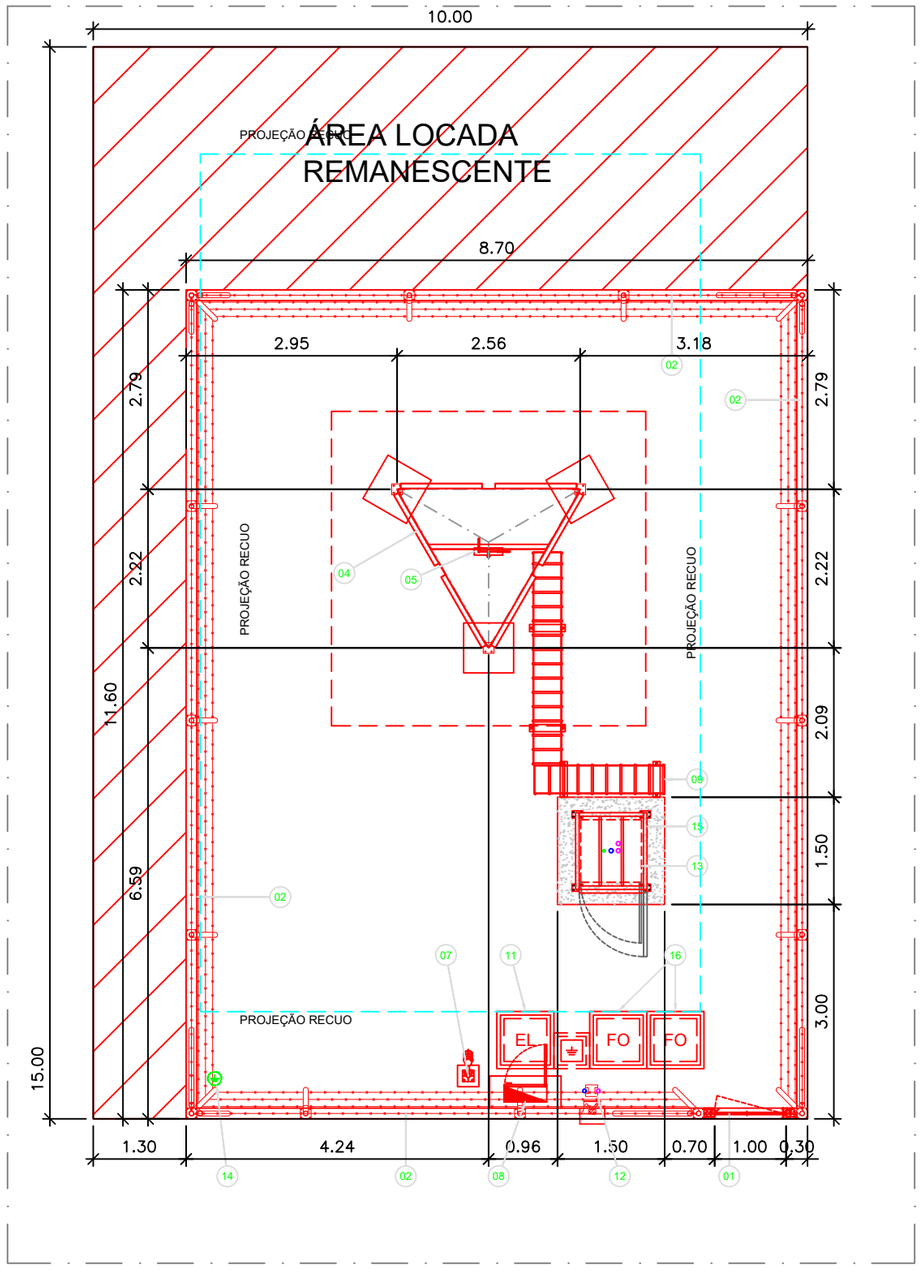


01 PLANTA BAIXA
ESCALA 1:75

LEGENDA:

1. PORTÃO DE PEDESTRE – EXISTENTE;
2. FECHAMENTO EM ALAMBRADO – A EXECUTAR;
3. PROJEÇÃO FUNDAÇÃO – A EXECUTAR;
4. TORRE METÁLICA h=30,00m – A INSTALAR;
5. ESCADA/COSTELA DE VACA DA EV;
6. PISO EM LASTRO DE BRITA N° 2 – A EXECUTAR;
7. LUMINÁRIA H=3,00m – A INSTALAR;
8. QUADRO QTME A INSTALAR EM ABRIGO DE ALVENARIA (ABERTURA PARA FACE FRONTAL DO SITE);
9. ESTEIRAMENTO L=400mm, h=300mm (PREVER INSTALAÇÃO DE COBERTURA METÁLICA NA ESTEIRA HORIZONTAL E VERTICAL ATÉ 15m) – A INSTALAR;
10. BASE EM CONCRETO PADRÃO PARA IMPLANTAÇÃO DO EQUIPAMENTO – A INSTALAR;
11. CAIXAS DE PASSAGEM EL/FO/AT – A INSTALAR;
12. ENTRADA DE ENERGIA EM ALVENARIA PARA 1 QM CONFORME PADRÃO DA CONCESSIONÁRIA LOCAL;
13. GABINETE TIPO 11 – A INSTALAR;
14. POÇO DE INSPEÇÃO DE ATERRAMENTO – A INSTALAR;
15. GRADIL PARA PROTEÇÃO DO EQUIPAMENTO – A INSTALAR;
16. CX. DE PASSAGEM FIBRA ÓPTICA PADRÃO VIVO – A EXECUTAR;

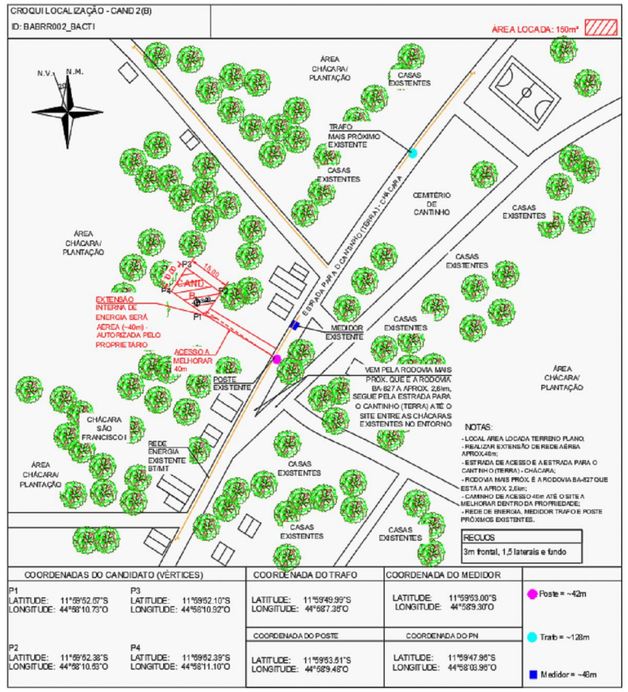

02 CROQUI DE SITUAÇÃO
SEM ESCALA

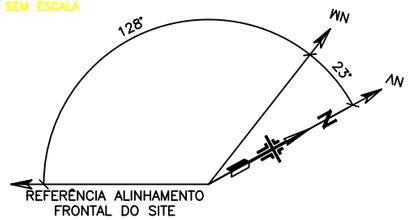

ATENÇÃO

1. ESTE PROJETO ESTÁ COMPATIBILIZADO COM O PROJETO DA FUNDAÇÃO;
2. NÃO REALIZAR SUPRESSÃO DA VEGETAÇÃO E REMOÇÃO DE ÁRVORES SEM A LICENÇA AMBIENTAL E AUTORIZAÇÃO DA WINITY
3. RECUOS A SEREM CONSIDERADOS DE ACORDO COM O SAR;
   EV E EQUIP: FRONTAL: 1,5m | LATERAL: 1,5m | FUNDOS: 1,5m

A entrega a terceiros e a reprodução deste documento, assim como o uso e a revelação do seu conteúdo, são proibidos, salvo por autorização expressa. Os infratores respondem por perdas e danos. No caso da concessão de patentes de invenção, modelos de utilidade, modelos ou desenhos industriais, ficam reservados os direitos de exclusividade

Pena	Esp.	Cor
1	0,15	7
2	0,25	7
3	0,20	7
4	0,15	7
5	0,40	7
6	0,50	7
7	0,20	7
8	0,15	7
9	0,10	7
10	0,15	1
20	0,15	1
30	0,20	7
80	0,15	3
98	0,20	98
142	0,15	142
170	0,15	5
210	0,15	6

ESCALA PLOT : 1/100
FORMATO ABNT A3 297x420

OBSERVAÇÕES:


1. MEDIDAS EM METROS.
2. VERIFICAR IN LOCO A NECESSIDADE DE PODA DE ÁRVORES LINDEIRAS À ÁREA LOCADA PARA INSTALAÇÃO DA EV.
3. PROJETO EXECUTIVO COMPATIBILIZADO COM O PROJETO DE FUNDAÇÃO: FORNECEDOR AGA ENGENHARIA. REV 00

COMENTÁRIO DE REVISÕES

REV.	DATA	DESCRIÇÃO	DESENHO	VERIFICAÇÃO
02	27/03/2026	COMPATIBILIZADO COM FUNDAÇÃO	FERA	WINITY
01	25/03/2026	ALTURA DAS ANTENAS	FERA	WINITY
00	16/03/2026	EMISSÃO INICIAL	FERA	WINITY

SOLICITANTE: vivo
CONCERSSIONÁRIA:
ENDEREÇO: **POVOADO CANTINHO DO SENHOR DOS AFLITOS, N°27 - BARREIRAS/BA - CEP: 47.809-999**
DETENTORA: winity TELECOM
COORDENADAS: **LAT.: 11°59'52.59"S LONG.: 44°58'10.46"W**
REVISÃO: 02
RESP. TÉC. EXECUÇÃO: F.E.R.A. PROJETOS E ENGENHARIA
PROJETO EXECUTIVO
SITE: BABRR002_C BACTI
EMISSÃO: 16/03/2026
ASSUNTO: PLANTA CIVIL
FOLHA: 02/15

FORMATO A3 (420x297mm)

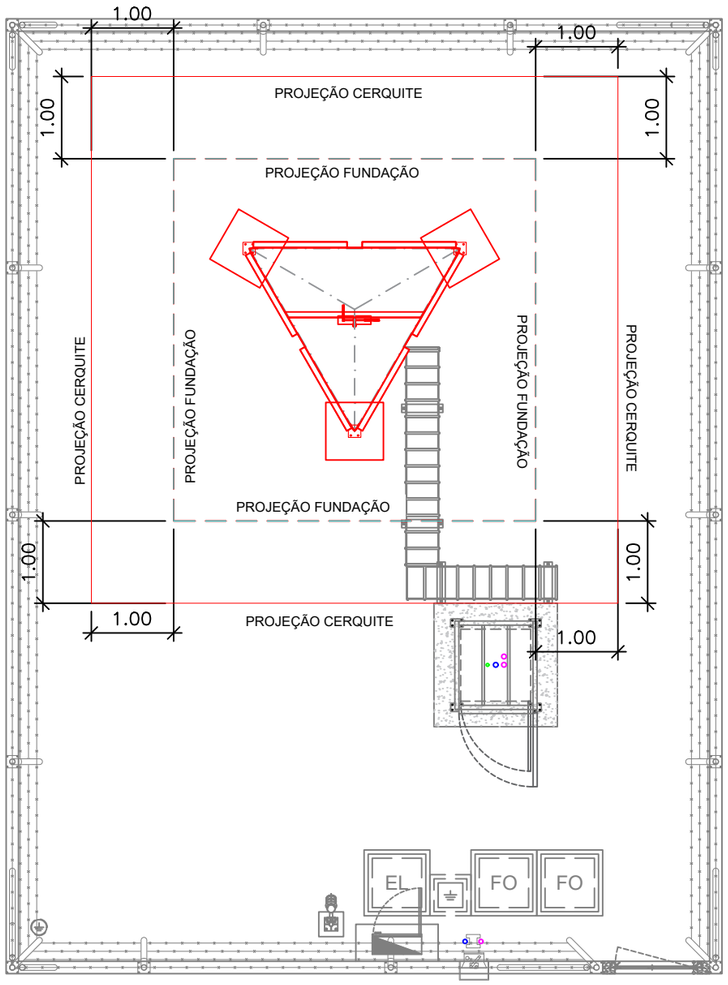

01 PLANTA BAIXA – DETALHE CERQUITE
ESCALA 1:75



02 FOTO ILUSTRAÇÃO CERQUITE:
SEM ESCALA

ISOLAMENTO DO CANTEIRO:

O CANTEIRO DE OBRA DEVERÁ SER ISOLADO EM TODO O SEU PERÍMETRO GARANTINDO DESTA FORMA QUE SOMENTE PESSOAS AUTORIZADAS POSSAM ACESSAR O CANTEIRO.

ISOLAMENTO PARA ESCAVAÇÕES:

DEVERÁ SER ISOLADO TODO O REDOR DA ESCAVAÇÃO COM CERQUITE GARANTINDO AS DISTANCIAS DE PROTEÇÃO MÍNIMA DE 1M (UM METRO) DA ESCAVAÇÃO.

É PREVISTO A ABERTURA PARCIAL PARA ACESSO DOS PROFISSIONAIS A ESCAVAÇÃO, BEM COMO A COLOCAÇÃO DA ESCADA PARA ACESSO DOS PROFISSIONAIS, A ABERTURA NÃO PODE ULTRAPASSAR 1M (UM METRO).

ISOLAMENTO PARA MONTAGEM DE EV:

OS LOCAIS ABAIXO DAS ATIVIDADES IÇAMENTO DE CARGA DEVERÃO SER ISOLADOS GARANTIDO QUE OS PROFISSIONAIS QUE NÃO ESTÃO ENVOLVIDOS NA ATIVIDADE FIQUEM EXPOSTOS AOS RISCOS DE QUEDA DE MATERIAL.

ISOLAMENTO EM CALÇADAS:

ATIVIDADES QUE ESTÃO SENDO REALIZADAS EM CALÇADAS DE ACESSO DE PEDESTRES DEVERÃO SER ISOLADAS GARANTINDO QUE PROFISSIONAIS EXTERNOS NÃO SE EXPONHAM AOS RISCOS DA ATIVIDADE, O ISOLAMENTO DEVERÁ ENVOLVER TODOS OS MATERIAIS QUE OCUPARAM A ÁREA EXTERNA DA OBRA.

A entrega a terceiros e a reprodução deste documento, assim como o uso e a revelação do seu conteúdo, são proibidos, salvo por autorização expressa. Os infratores respondem por perdas e danos. No caso da concessão de patentes de invenção, modelos de utilidade, modelos ou desenhos industriais, ficam reservados os direitos de exclusividade

Pena	Esp.	Cor
1	0,15	7
2	0,25	7
3	0,20	7
4	0,15	7
5	0,40	7
6	0,50	7
7	0,20	7
8	0,15	7
9	0,10	7
10	0,15	1
20	0,15	1
30	0,20	7
80	0,15	3
98	0,20	98
142	0,15	142
170	0,15	5
210	0,15	6

ESCALA PLOT : 1/100
FORMATO ABNT A3 297x420

FORMATO A3 (420x297mm)

OBSERVAÇÕES:


1 – MEDIDAS EM METROS

COMENTÁRIO DE REVISÕES


REV.	DATA	DESCRIÇÃO	DESENHO	VERIFICAÇÃO
02	27/03/2026	COMPATIBILIZADO COM FUNDAÇÃO	FERA	WINITY
01	25/03/2026	ALTURA DAS ANTENAS	FERA	WINITY
00	16/03/2026	EMISSÃO INICIAL	FERA	WINITY

SOLICITANTE: vivo
CONCERSSIONÁRIA:
ENDEREÇO: POVOADO CANTINHO DO SENHOR DOS AFLITOS, N°27 - BARREIRAS/BA - CEP: 47.809-999
DETENTORA: winity TELECOM
COORDENADAS: LAT.: 11°59'52.59"S LONG.: 44°58'10.46"W
REVISÃO: 02
RESP. TÉC. EXECUÇÃO: F.E.R.A. PROJETOS E ENGENHARIA
PROJETO EXECUTIVO
SITE: BABRR002_C BACTI
EMISSÃO: 16/03/2026
ASSUNTO: PLANTA CIVIL – FECHAMENTO CERQUITE
FOLHA: 03/15


CARREGAMENTO ANTENAS VIVO À INSTALAR													
ALTURA	SETOR	TIPO DE ANTENA	MODELO	DIMENSÕES (mm)						AZIMUTE (N.V.)	QUANT.	ÁREA DE EXPOSIÇÃO (m²)	ARRASTO	ÁREA DE EXPOSIÇÃO (m²)
30,0000	ALPHA	RF	Antenna 4805 2L4M 1.5m	1500	x	488	x	–		0°/120°/240°	3	2.196	1.2	2.635
30,0000	–	RRU	RRU2271	409	x	269	x	–		–	3	0.330	1.2	0.396
28,5000	–	ODU	XMC-5D	210	x	210	x	0		–	1	0.044	1.2	0.053
28,5000	–	MW	SCX3-W60AH				–	0.90		165°	01	0.640	1.6	1.02
										TOTAL SEM ARRASTO		3.404	TOTAL C/ ARRASTO	4.337

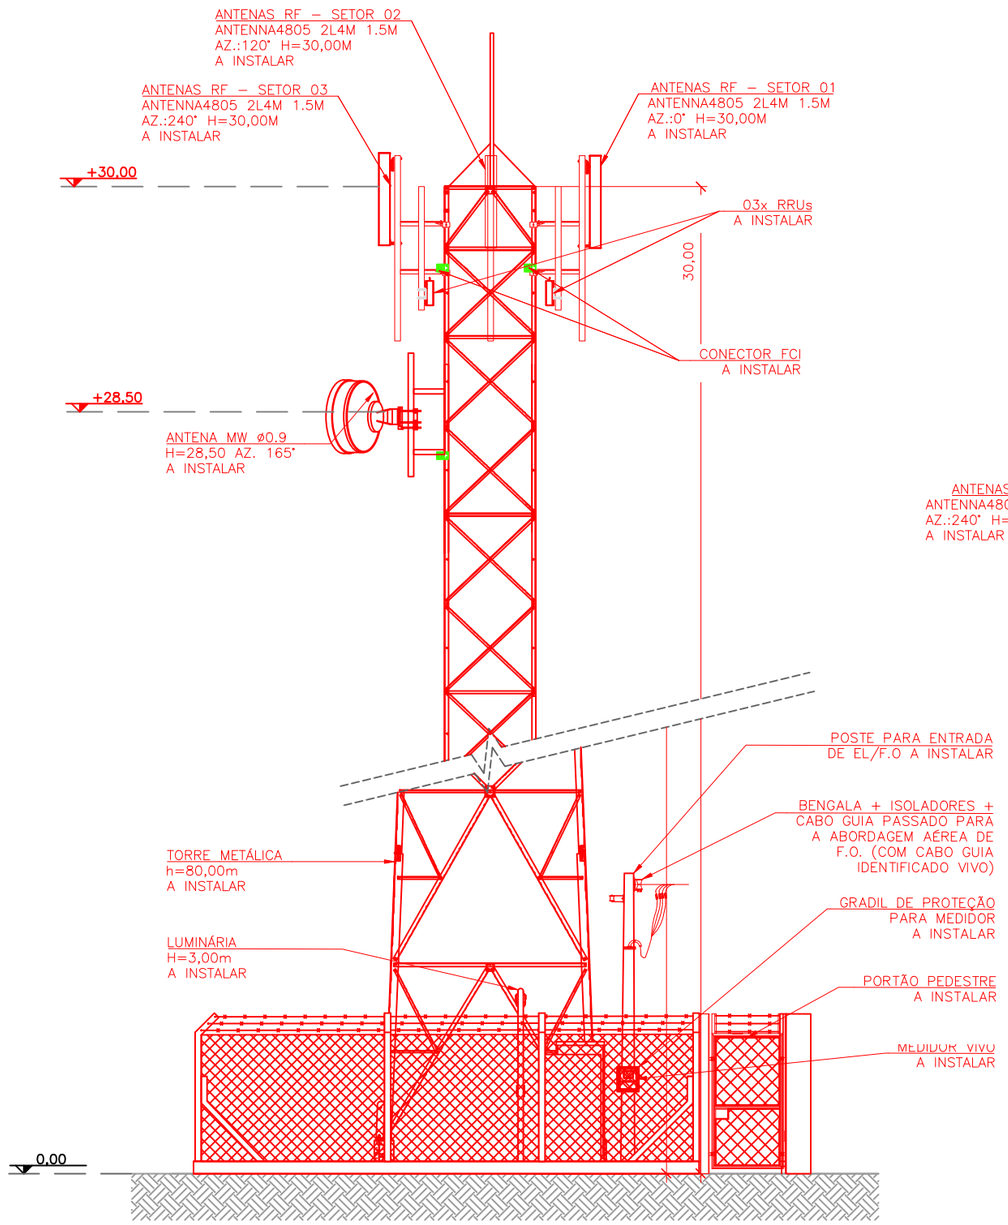


01 ELEVAÇÃO
ESCALA 1:100

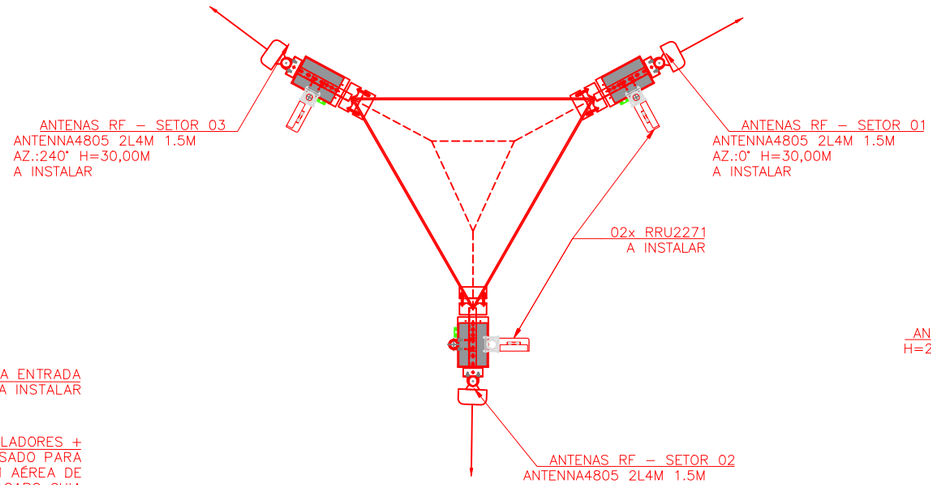

02 SETORIZAÇÃO RF
SEM ESCALA

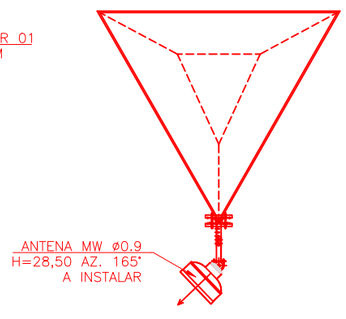

03 SETORIZAÇÃO MW
SEM ESCALA

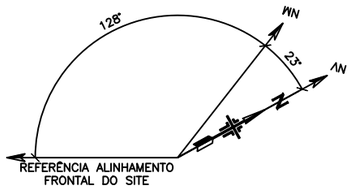

Pena	Esp.	Cor
1	0,15	7
2	0,25	7
3	0,20	7
4	0,15	7
5	0,40	7
6	0,50	7
7	0,20	7
8	0,15	7
9	0,10	7
10	0,15	1
20	0,15	1
30	0,20	7
80	0,15	3
98	0,20	98
142	0,15	142
170	0,15	5
210	0,15	6

ESCALA PLOT : 1/100
FORMATO ABNT A3 297x420

A entrega a terceiros e a reprodução deste documento, assim como o uso e a revelação do seu conteúdo, são proibidos, salvo por autorização expressa. Os infratores respondem por perdas e danos. No caso da concessão de patentes de invenção, modelos de utilidade, modelos ou desenhos industriais, ficam reservados os direitos de exclusividade

OBSERVAÇÕES:

1 – MEDIDAS EM METROS

COMENTÁRIO DE REVISÕES

REV.	DATA	DESCRIÇÃO	DESENHO	VERIFICAÇÃO
02	27/03/2026	COMPATIBILIZADO COM FUNDAÇÃO	FERA	WINITY
01	25/03/2026	ALTURA DAS ANTENAS	FERA	WINITY
00	16/03/2026	EMISSÃO INICIAL	FERA	WINITY

SOLICITANTE: vivo

CONCERSSIONÁRIA:

ENDEREÇO: POVOADO CANTINHO DO SENHOR DOS AFLITOS, N°27 - BARREIRAS/BA - CEP: 47.809-999

DETENTORA: winity TELECOM

COORDENADAS: LAT.: 11°59'52.59"S LONG.: 44°58'10.46"W

REVISÃO: 02

RESP. TÉC. EXECUÇÃO: F.E.R.A. PROJETOS E ENGENHARIA

PROJETO EXECUTIVO


SITE: BABRR002_C BACTI


EMISSÃO: 16/03/2026


ASSUNTO: PLANTA CIVIL – FECHAMENTO CERQUITE


FOLHA: 04/15


FORMATO A3 (420x297mm)

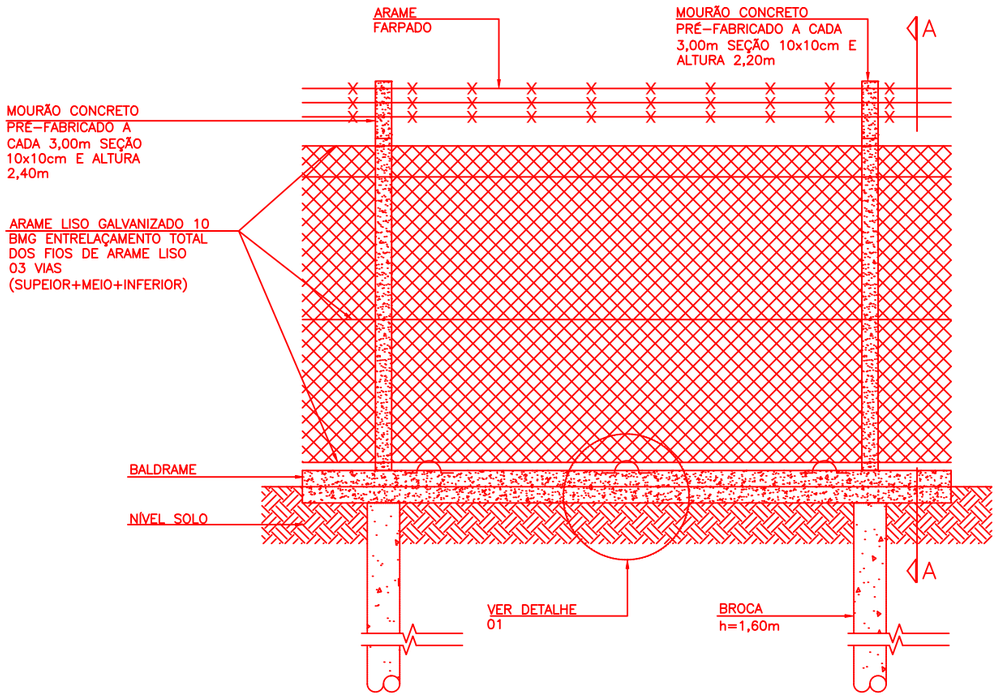


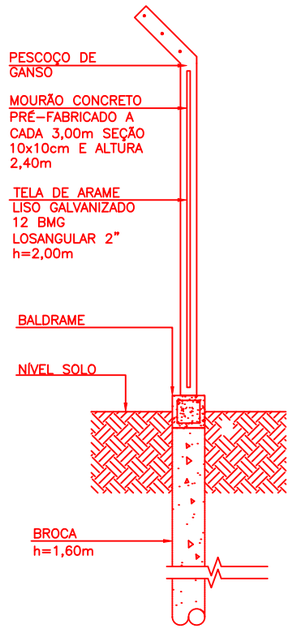


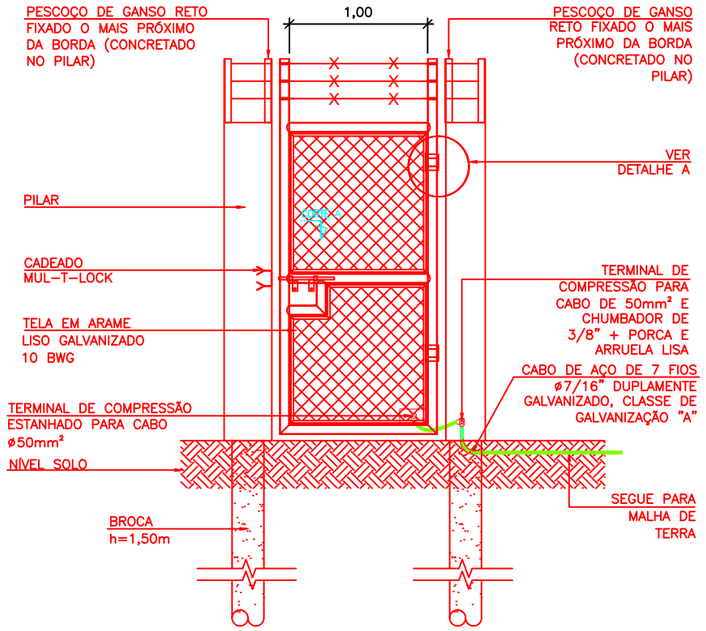


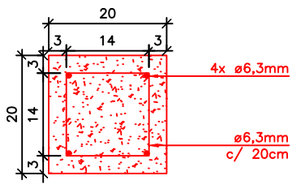


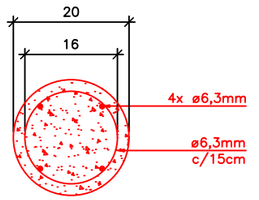

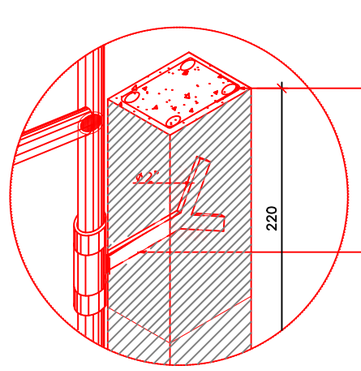

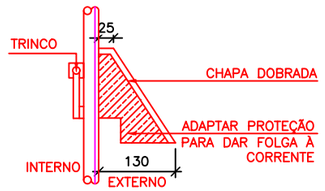

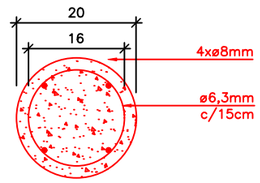

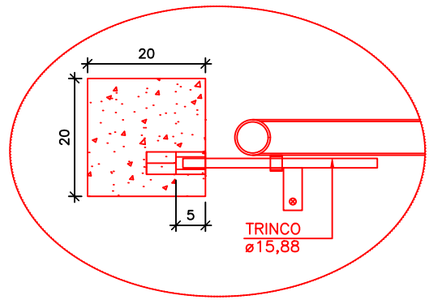

A entrega a terceiros e a reprodução deste documento, assim como o uso e a revelação do seu conteúdo, são proibidos, salvo por autorização expressa. Os infratores respondem por perdas e danos. No caso da concessão de patentes de invenção, modelos de utilidade, modelos ou desenhos industriais, ficam reservados os direitos de exclusividade

Pena	Esp.	Cor
1	0,15	7
2	0,25	7
3	0,20	7
4	0,15	7
5	0,40	7
6	0,50	7
7	0,20	7
8	0,15	7
9	0,10	7
10	0,15	1
20	0,15	1
30	0,20	7
80	0,15	3
98	0,20	98
142	0,15	142
170	0,15	5
210	0,15	6

ESCALA PLOT. : 1/100
FORMATO ABNT A3 297x420

OBSERVAÇÕES:

1 – MEDIDAS EM METROS

COMENTÁRIO DE REVISÕES

REV.	DATA	DESCRIÇÃO	DESENHO	VERIFICAÇÃO
02	27/03/2026	COMPATIBILIZADO COM FUNDAÇÃO	FERA	WINITY
01	25/03/2026	ALTURA DAS ANTENAS	FERA	WINITY
00	16/03/2026	EMISSÃO INICIAL	FERA	WINITY

SOLICITANTE: vivo

CONCERSSIONÁRIA:

ENDEREÇO: **POVOADO CANTINHO DO SENHOR DOS AFLITOS, N°27 - BARREIRAS/BA - CEP: 47.809-999**

DETENTORA: winity TELECOM

COORDENADAS: **LAT.: 11°59'52.59"S LONG.: 44°58'10.46"W**

REVISÃO: 02

RESP. TÉC. EXECUÇÃO: F.E.R.A. PROJETOS E ENGENHARIA

PROJETO EXECUTIVO


SITE: BABRR002_C BACTI

EMISSÃO: 16/03/2026


ASSUNTO: FECHAMENTO EM ALAMBRADO

FOLHA: 05/15


FORMATO A3 (420x297mm)

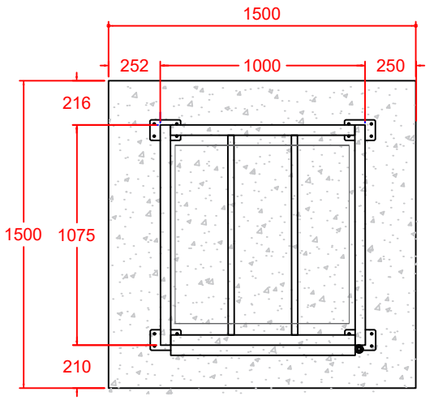


PLANTA BAIXA – LAYOUT BASE DE CONCRETO
SEM ESCALA

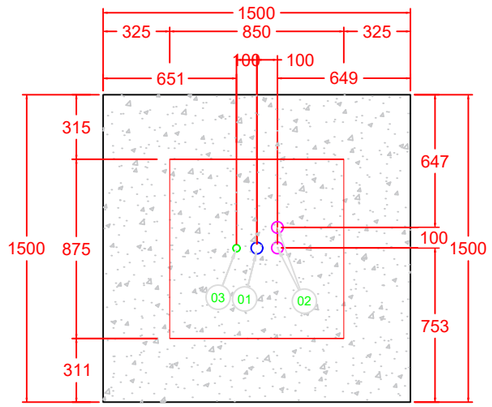

DETALHE FURAÇÕES NA BASE DE CONCRETO
SEM ESCALA

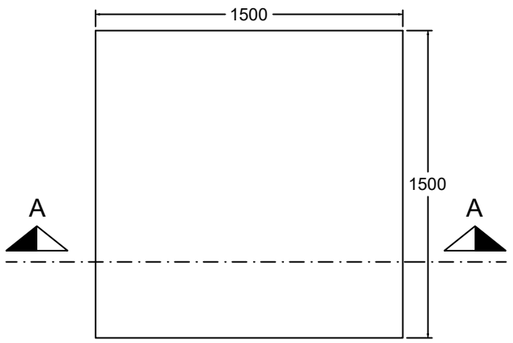

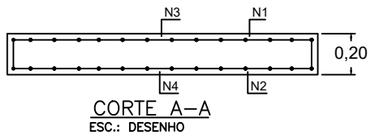

CORTE A–A
ESC.: DESENHO

N1=N2=N3=N4 (4x)9ø8.0 c/16cm C=1,04 (SUP/INF)

01 BASE DE EQUIPAMENTOS
SEM ESCALA

LEGENDA:


① ELETRODUTO KANAFLEX ø2"PARA ELETRICA
② ELETRODUTO KANAFLEX ø2" PARA FO
③ ELETRODUTO KANAFLEX ø1"PARA ATERRAMENTO

NOTAS:


1 - MEDIDAS EM METROS EXCETO ONDE INDICADO
2 - COBRIMENTO 3cm
3 - CONCRETO ESTRUTURAL fck=20 MPa
4 - AÇO CA-50

NOTAS:

Grupo Alfa – Gabinete Tipo 11AE – Revisão 00 – 18/04/2023; SR 4,5U 23" 200A –48V 12kW – Revisão 00 – 26/04/2023; PDU 3U 23" 200A 48V (+) e (–) Telefonica – Revisão 00 – 20/04/2023.

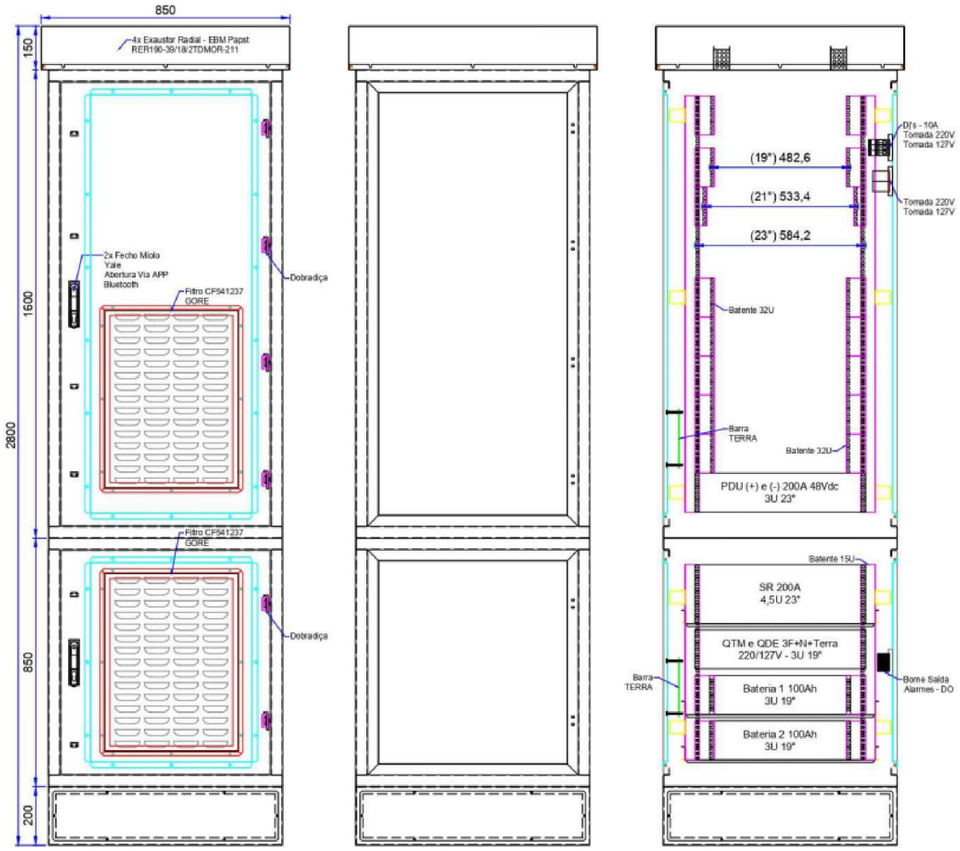

Vista Frontal | Vista Frontal Sem Porta | Vista Frontal Interna

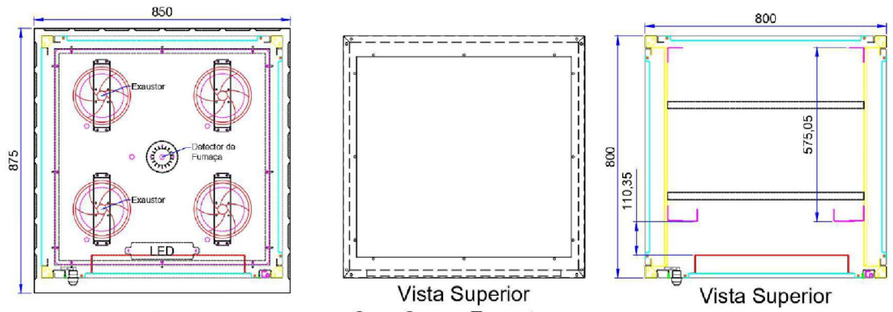

Vista Superior | Vista Superior Sem Comp. Exaustores | Vista Superior Interna

02 DETALHES GABINETE TIPO 11 – GRUPO ALFA
SEM ESCALA

Pena	Esp.	Cor
1	0,15	7
2	0,25	7
3	0,20	7
4	0,15	7
5	0,40	7
6	0,50	7
7	0,20	7
8	0,15	7
9	0,10	7
10	0,15	1
20	0,15	1
30	0,20	7
80	0,15	3
98	0,20	98
142	0,15	142
170	0,15	5
210	0,15	6

ESCALA PLOT : 1/100
FORMATO ABNT A3 297x420

OBSERVAÇÕES:


COMENTÁRIO DE REVISÕES

REV.	DATA	DESCRIÇÃO	DESENHO	VERIFICAÇÃO
02	27/03/2026	COMPATIBILIZADO COM FUNDAÇÃO	FERA	WINITY
01	25/03/2026	ALTURA DAS ANTENAS	FERA	WINITY
00	16/03/2026	EMISSÃO INICIAL	FERA	WINITY


SOLICITANTE: vivo
CONCERSSIONÁRIA:
ENDEREÇO: POVOADO CANTINHO DO SENHOR DOS AFLITOS, N°27 - BARREIRAS/BA - CEP: 47.809-999
DETENTORA: winity TELECOM
COORDENADAS: LAT.: 11°59'52.59"S LONG.: 44°58'10.46"W
REVISÃO: 02
RESP. TÉC. EXECUÇÃO: F.E.R.A. PROJETOS E ENGENHARIA
PROJETO EXECUTIVO
SITE: BABRR002_C BACTI
EMISSÃO: 16/03/2026
ASSUNTO: DETALHE BASE DE EQUIPAMENTOS
FOLHA: 06/15

FORMATO A3 (420x297mm)


A entrega a terceiros e a reprodução deste documento, assim como o uso e a revelação do seu conteúdo, são proibidos, salvo por autorização expressa. Os infratores respondem por perdas e danos. No caso da concessão de patentes de invenção, modelos de utilidade, modelos ou desenhos industriais, ficam reservados os direitos de exclusividade

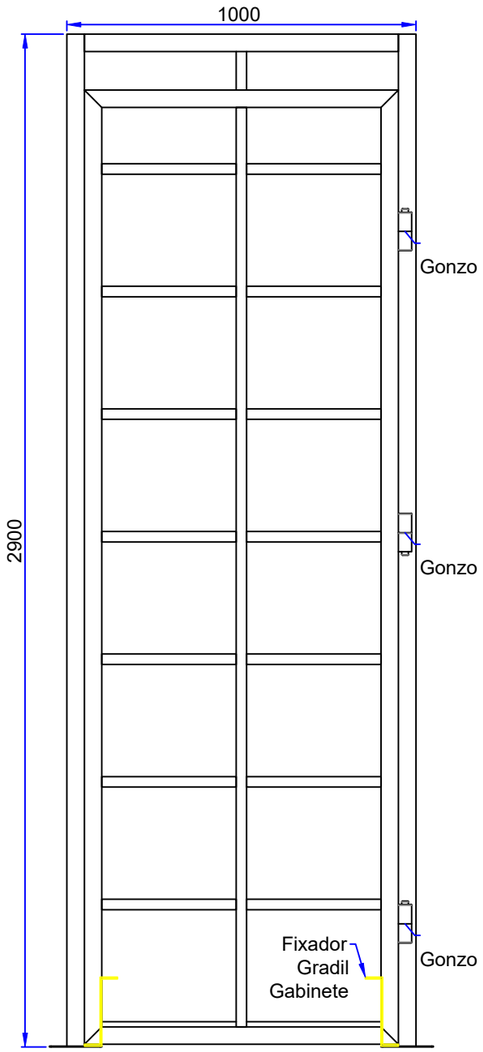


Vista Frontal
Com Portas
sem escala

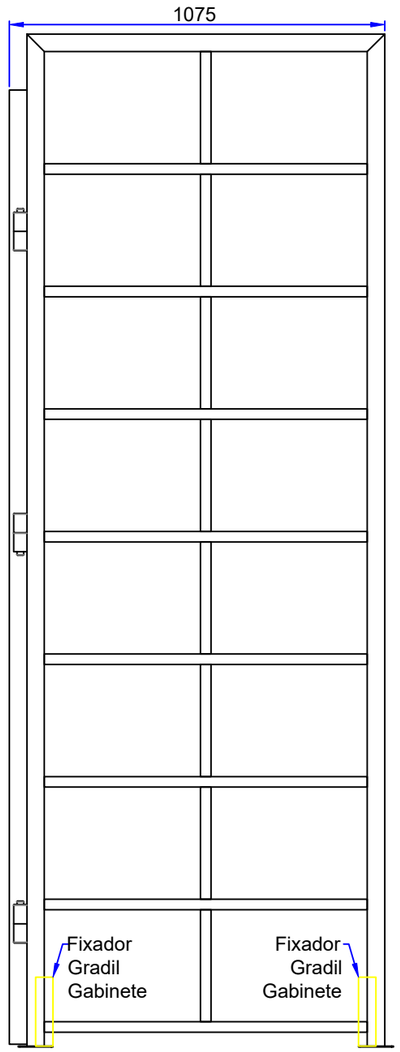

Vista Lateral
sem escala

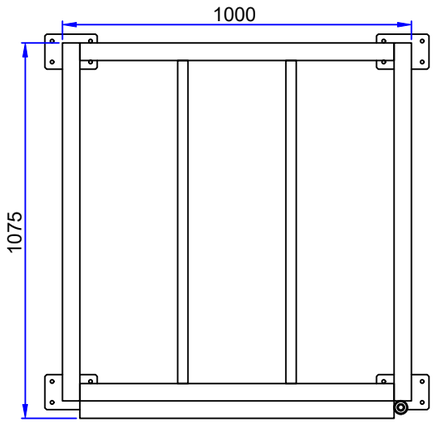

Vista Superior
sem escala

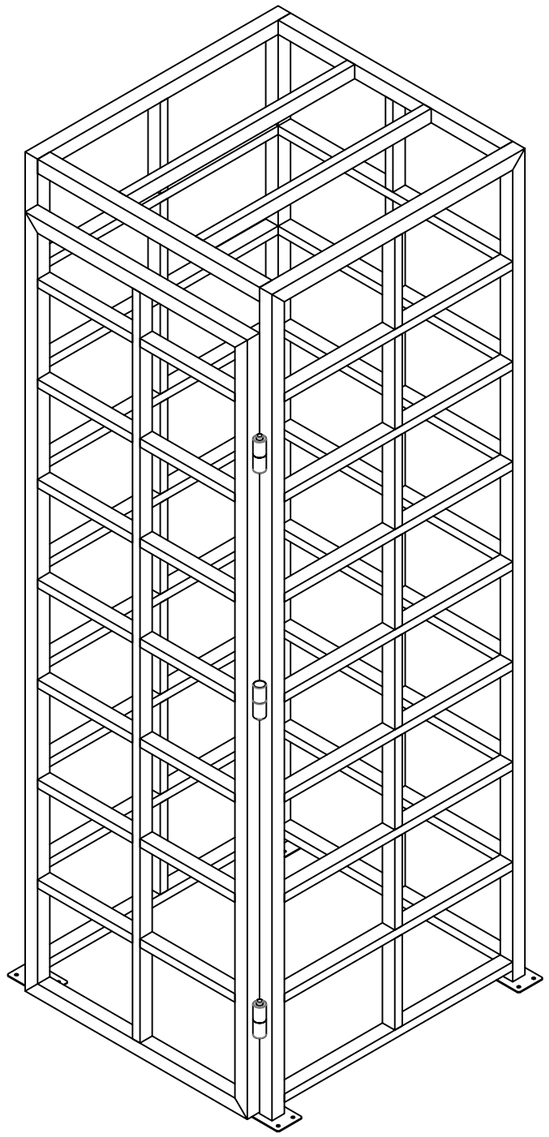

Perspectiva
sem escala

A entrega a terceiros e a reprodução deste documento, assim como o uso e a revelação do seu conteúdo, são proibidos, salvo por autorização expressa. Os infratores respondem por perdas e danos. No caso da concessão de patentes de invenção, modelos de utilidade, modelos ou desenhos industriais, ficam reservados os direitos de exclusividade

Pena	Esp.	Cor
1	0,15	7
2	0,25	7
3	0,20	7
4	0,15	7
5	0,40	7
6	0,50	7
7	0,20	7
8	0,15	7
9	0,10	7
10	0,15	1
20	0,15	1
30	0,20	7
80	0,15	3
98	0,20	98
142	0,15	142
170	0,15	5
210	0,15	6

ESCALA PLOT : 1/100
FORMATO ABNT A3 297x420

OBSERVAÇÕES:

COMENTÁRIO DE REVISÕES

REV.	DATA	DESCRIÇÃO	DESENHO	VERIFICAÇÃO
02	27/03/2026	COMPATIBILIZADO COM FUNDAÇÃO	FERA	WINITY
01	25/03/2026	ALTURA DAS ANTENAS	FERA	WINITY
00	16/03/2026	EMISSÃO INICIAL	FERA	WINITY

SOLICITANTE: vivo

CONCERSSIONÁRIA:

ENDEREÇO: **POVOADO CANTINHO DO SENHOR DOS AFLITOS, N°27 - BARREIRAS/BA - CEP: 47.809-999**

DETENTORA: winity TELECOM

COORDENADAS:
LAT.: 11°59'52.59"S
LONG.: 44°58'10.46"W

REVISÃO: 02

RESP. TÉC. EXECUÇÃO: F.E.R.A. PROJETOS E ENGENHARIA

PROJETO EXECUTIVO


SITE: BABRR002_C BACTI


EMISSÃO: 16/03/2026


ASSUNTO: GRADIL DE PROTEÇÃO DOS EQUIPAMENTOS

FOLHA: 07/15

FORMATO A3 (420x297mm)

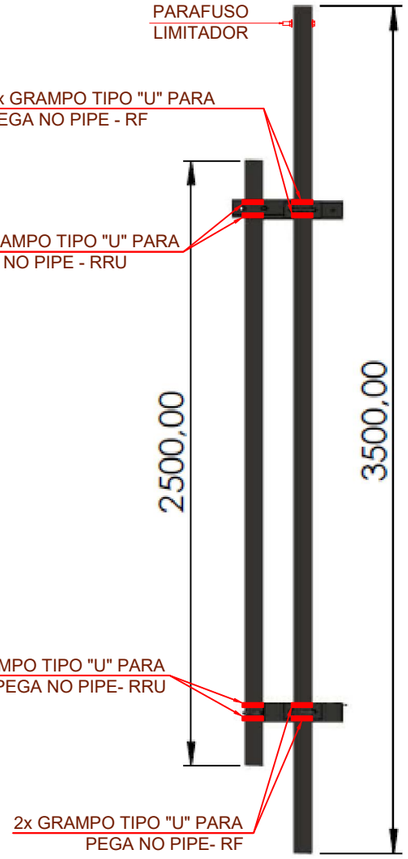

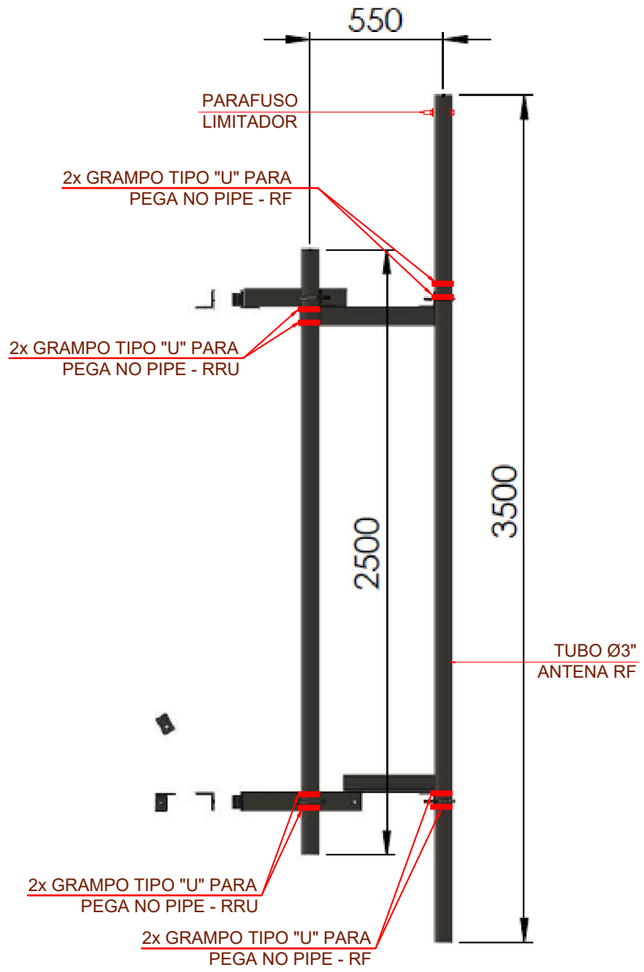


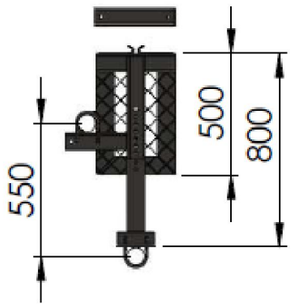

NOTAS:

SUPORTES DE ANTENAS ø3" X 3,50M

ESTABELECER ESTRUTURAS DE RRUS DE DIMENSÕES ø3" X 2,00M CONFECCIONADAS PARA SUPORTAR A INSTALAÇÃO MÍNIMA DE 02 (DOIS) CONJUNTOS DE 03 (TRÊS) RRUS.

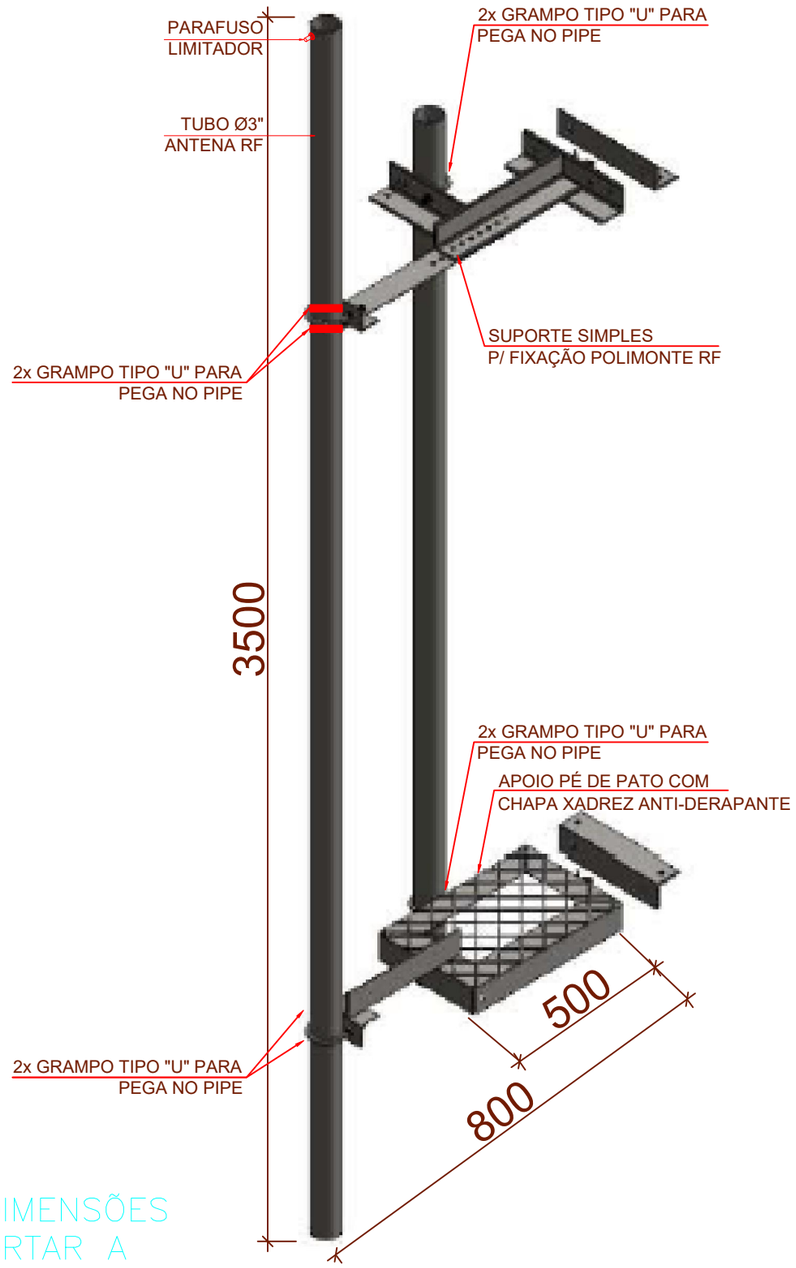

A entrega a terceiros e a reprodução deste documento, assim como o uso e a revelação do seu conteúdo, são proibidos, salvo por autorização expressa. Os infratores respondem por perdas e danos. No caso da concessão de patentes de invenção, modelos de utilidade, modelos ou desenhos industriais, ficam reservados os direitos de exclusividade

Pena	Esp.	Cor
1	0,15	7
2	0,25	7
3	0,20	7
4	0,15	7
5	0,40	7
6	0,50	7
7	0,20	7
8	0,15	7
9	0,10	7
10	0,15	1
20	0,15	1
30	0,20	7
80	0,15	3
98	0,20	98
142	0,15	142
170	0,15	5
210	0,15	6

ESCALA PLOT : 1/100
FORMATO ABNT A3 297x420

FORMATO A3 (420x297mm)

OBSERVAÇÕES:

COMENTÁRIO DE REVISÕES

REV.	DATA	DESCRIÇÃO	DESENHO	VERIFICAÇÃO
02	27/03/2026	COMPATIBILIZADO COM FUNDAÇÃO	FERA	WINITY
01	25/03/2026	ALTURA DAS ANTENAS	FERA	WINITY
00	16/03/2026	EMISSÃO INICIAL	FERA	WINITY

SOLICITANTE: vivo

CONCERSSIONÁRIA:

ENDEREÇO: **POVOADO CANTINHO DO SENHOR DOS AFLITOS, N°27 - BARREIRAS/BA - CEP: 47.809-999**

DETENTORA: winity TELECOM

COORDENADAS: **LAT.: 11°59'52.59"S LONG.: 44°58'10.46"W**

REVISÃO: 02

RESP. TÉC. EXECUÇÃO: F.E.R.A. PROJETOS E ENGENHARIA


PROJETO EXECUTIVO

SITE: BABRR002_C BACTI

EMISSÃO: 16/03/2026

ASSUNTO: DETALHE SUPORTE DE RF

FOLHA: 08/15

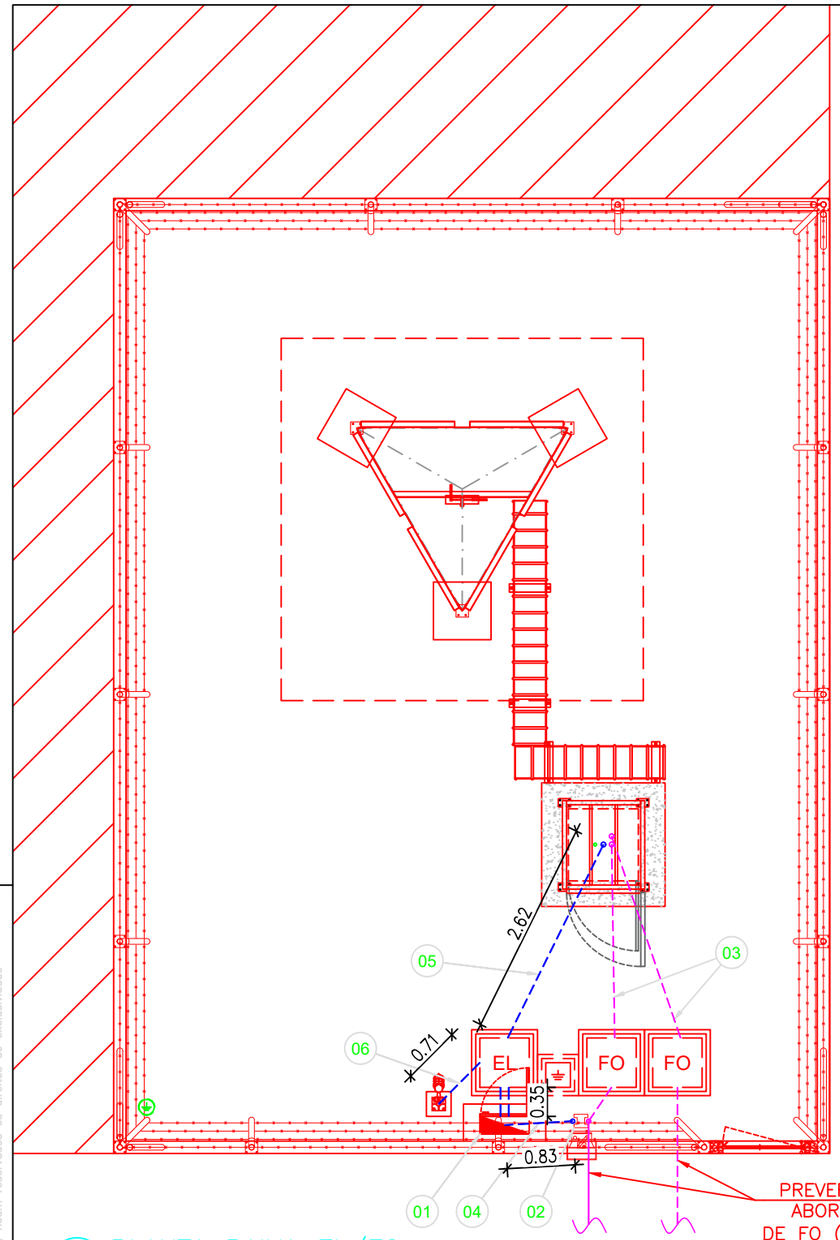

01 PLANTA BAIXA EL/FO
ESCALA 1:75

DIMENSIONAMENTO CABOS

$$Fórmula\ Adotada\ 2F-127/220V\ Conforme\ Especif.\ Técnica$$
$$V\% = \frac{In \times L \times 2}{56 \times S} \times \frac{100}{V}$$

$$Fórmula\ Adotada\ 2F-220V\ Conforme\ Especif.\ Técnica$$
$$\Delta V\% = \frac{In \times L \times 2}{56 \times S} \times \frac{100}{V}$$

TABELA DE CABOS CA

Circ.	De	Para	Distância (m)	Tensão (V)	Corrente (A)	Número de Fases	Condutor 750VD (mm²)							Queda de Tensão (%)	Proteção (A)
							Tipo	qt.	Fase	qt.	Neutro	qt.	Terra		
1	QM	QTME	4,83	220	63	3	KANAFLEX	3	16	1	16	1	16	0,31	63
2	QTME	EQUIPAMENTO	9,20	220	63	3	KANAFLEX	3	16	1	16	1	16	0,59	63
3	QTME	LUMINARIA	7,56	220	10	1	KANAFLEX	1	2,5	1	2,5	1	2,5	0,49	10
											TOTAL			**1,39**	%

*Prever folga de cabos de aproximadamente 3,0m.

BA - Bahia | Barreiras

COELBA	
Tensão Nominal 1	440/220 volts
Tensão Nominal 2	380/220 volts

FONTE: ANEEL.GOV.BR

LEGENDA:

1. QUADRO QTME A INSTALAR EM ABRIGO DE ALVENARIA;
2. POSTE PADRÃO, CONFORME CONCESSIONÁRIA LOCAL;
3. FO ø2" KANAFLEX A INSTALAR COM ARAME–GUIA
4. 3F+N+T (#16mm²/750V – CABOS DE COBRE) EM ELETRODUTO KANAFLEX ø2'' – CIRCUITO ENTERRADO – A INSTALAR (SAI DO QM VAI ATÉ O QMTE)
5. 3F+N+T (#16mm²/750V – CABOS DE COBRE) EM ELETRODUTO KANAFLEX ø2'' A INSTALAR (SAI DO QMTE VAI ATÉ OS EQUIPAMENTOS)
6. CABO PP 2,5mm² PARA LUMINÁRIA EM ELETRODUTO PVC ø1"

ELETRODUTO DE KANAFLEX ø 2" (ENVELOPADO)

01 DETALHE DO ELETRODUTO ENVELOPADO
SEM ESCALA

Pena	Esp.	Cor	
1	0,15	7	
2	0,25	7	
3	0,20	7	
4	0,15	7	
5	0,40	7	
6	0,50	7	
7	0,20	7	
8	0,15	7	
9	0,10	7	
10	0,15	1	
20	0,15	1	
30	0,20	7	
80	0,15	3	
98	0,20	98	
142	0,15	142	
170	0,15	5	
210	0,15	6	

ESCALA PLOT. : 1/100
FORMATO ABNT A3 297x420

FORMATO A3 (420x297mm)

OBSERVAÇÕES:


1. MEDIDAS EM METROS.

COMENTÁRIO DE REVISÕES


REV.	DATA	DESCRIÇÃO	DESENHO	VERIFICAÇÃO
02	27/03/2026	COMPATIBILIZADO COM FUNDAÇÃO	FERA	WINITY
01	25/03/2026	ALTURA DAS ANTENAS	FERA	WINITY
00	16/03/2026	EMISSÃO INICIAL	FERA	WINITY

SOLICITANTE: vivo
CONCERSSIONÁRIA:
ENDEREÇO: **POVOADO CANTINHO DO SENHOR DOS AFLITOS, N°27 - BARREIRAS/BA - CEP: 47.809-999**
DETENTORA: winity TELECOM
COORDENADAS: **LAT.: 11°59'52.59"S LONG.: 44°58'10.46"W**
REVISÃO: 02
RESP. TÉC. EXECUÇÃO: F.E.R.A. PROJETOS E ENGENHARIA
PROJETO EXECUTIVO
SITE: BABRR002_C BACTI
EMISSÃO: 16/03/2026
ASSUNTO: PLANTA ELÉTRICA
FOLHA: 09/15


A entrega a terceiros e a reprodução deste documento, assim como o uso e a revelação do seu conteúdo, são proibidos, salvo por autorização expressa. Os infratores respondem por perdas e danos. No caso da concessão de patentes de invenção, modelos de utilidade, modelos ou desenhos industriais, ficam reservados os direitos de exclusividade

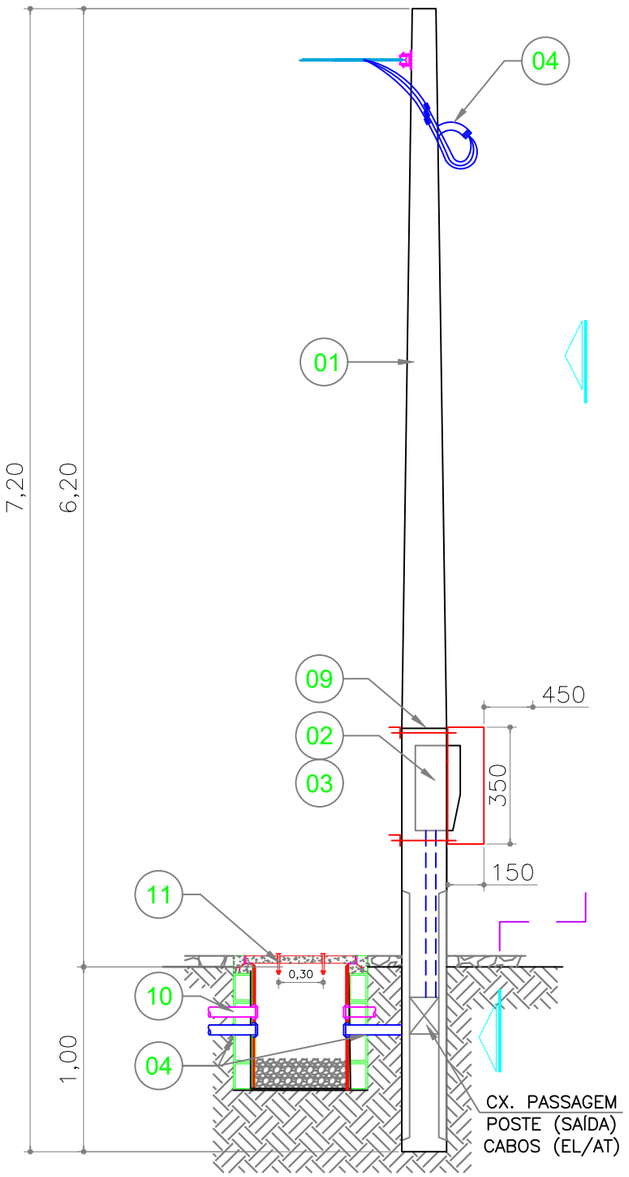

VISTA LATERAL

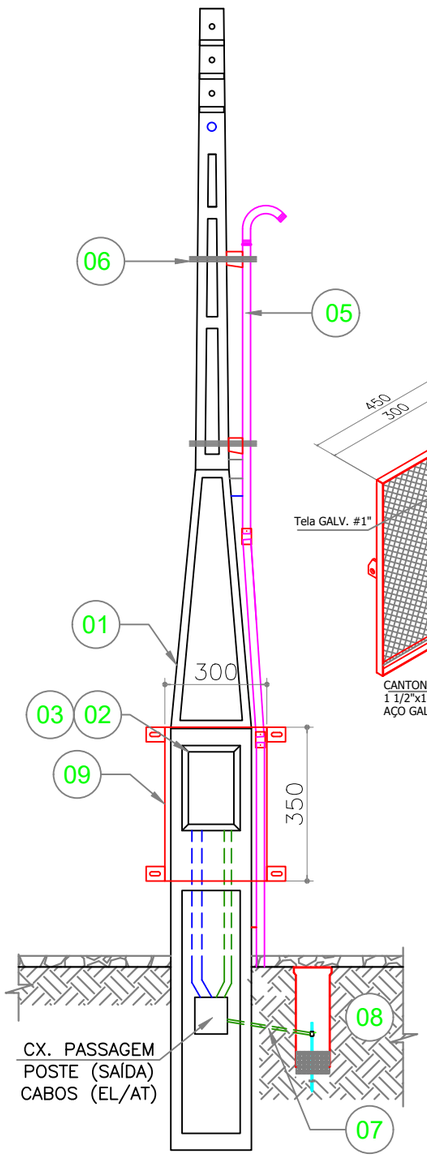


VISTA FRONTAL

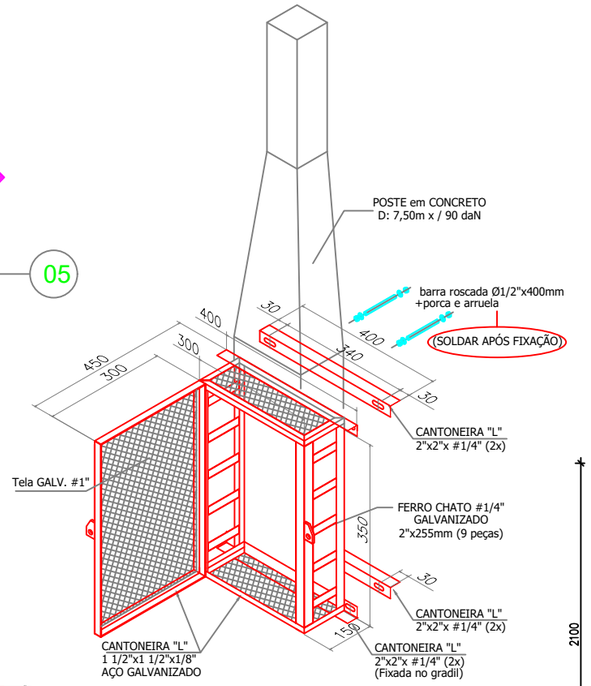


LEGENDA QTM VIVO

ITEM	DESCRIÇÃO DO MATERIAL
A	ABRIGO EM ALVENARIA PARA QTM VIVO
B	QTM VIVO
C	ATERRAMENTO (ELETRODUTO PVC RÍGIDO Ø3/4")
D	ILUMINAÇÃO EXTERNA (ELETRODUTO PVC RÍGIDO Ø3/4")
E	BTS (ELETRODUTO PVC RÍGIDO Ø2")
F	ELETRODUTO DE PVC RÍGIDO Ø1"
G	SEALTUBE Ø1" PARA PROTEÇÃO DOS CABOS EL
H	ALIMENTAÇÃO (ELETRODUTO PVC RÍGIDO Ø2")
I	PINGADEIRA EM ALVENARIA (IMPERMEABILIZADA)
J	GRADE DE PROTEÇÃO METÁLICA C/ CADEADO SEGREDO
K	CÉLULA FOTOELÉTRICA PARA USO EXTERNO

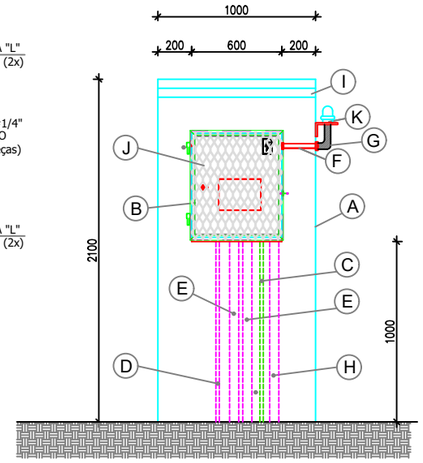

VISTA FRONTAL
SEM ESCALA

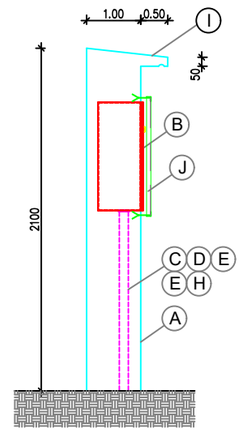

VISTA LATERAL
SEM ESCALA

LEGENDA:

01 POSTE–ENT. ENERGIA EM CONCRETO ARMADO (H:7,50m)
CONFORME PADRÃO DA CONCESSIONÁRIA LOCAL

02 CAIXA PARA MEDIDOR – CONFORME PADRÃO DA CONCESSIONÁRIA LOCAL

03 DISJUNTOR TERMOMAGNÉTICO

04 ELETRODUTO KANAFLEX ø2" – (EL)

05 ELETRODUTO FGFø2" + CURVA FGFø2" x 135° – (F.O.)
BENGALA + IDOLADORES + CABO GUIA PARA A ABORDAGEM
AEREA DE (FO) NA IMPLANTAÇÃO CIVIL

06 FITA MATÁLICA (ALUMINIO) FIXAÇÃO ELETRODUTO (F.O.)


07 ATERRAMENTO DO MEDIDOR – CABO COBRE VERDE #50mm2
EM ELETRODUTO KANAFLEX ø1"

08 POÇO DE INSPEÇÃO + HASTE DE ATERRAMENTO TIPO
TIPO COPPERWELD Ø3/4"x3,00m

09 GRADIL DE PROTEÇÃO (ANTIVANDALISMO)– MEDIDOR

10 ELETRODUTO KANAFLEX ø2" – (FO)

11 CX. PASSAGEM em ALVENARIA– (EL/FO)

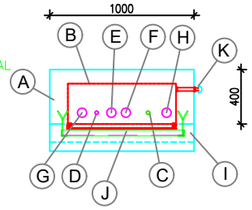

PLANTA
SEM ESCALA

1 PADRÃO DE ENTRADA DE ENERGIA
SEM ESCALA

Pena	Esp.	Cor
1	0,15	7
2	0,25	7
3	0,20	7
4	0,15	7
5	0,40	7
6	0,50	7
7	0,20	7
8	0,15	7
9	0,10	7
10	0,15	1
20	0,15	1
30	0,20	7
80	0,15	3
98	0,20	98
142	0,15	142
170	0,15	5
210	0,15	6

ESCALA PLOT : 1/100
FORMATO ABNT A3 297x420

FORMATO A3 (420x297mm)


OBSERVAÇÕES:

COMENTÁRIO DE REVISÕES

REV.	DATA	DESCRIÇÃO	DESENHO	VERIFICAÇÃO
02	27/03/2026	COMPATIBILIZADO COM FUNDAÇÃO	FERA	WINITY
01	25/03/2026	ALTURA DAS ANTENAS	FERA	WINITY
00	16/03/2026	EMISSÃO INICIAL	FERA	WINITY

SOLICITANTE: vivo
CONCERSSIONÁRIA:
ENDEREÇO: **POVOADO CANTINHO DO SENHOR DOS AFLITOS, N°27 - BARREIRAS/BA - CEP: 47.809-999**
DETENTORA: winity TELECOM
COORDENADAS: **LAT.: 11°59'52.59"S LONG.: 44°58'10.46"W**
REVISÃO: 02
RESP. TÉC. EXECUÇÃO: F.E.R.A. PROJETOS E ENGENHARIA
PROJETO EXECUTIVO
SITE: BABRR002_C BACTI
EMISSÃO: 16/03/2026
ASSUNTO: ENTRADA DE ENERGIA
FOLHA: 10/15


A entrega a terceiros e a reprodução deste documento, assim como o uso e a revelação do seu conteúdo, são proibidos, salvo por autorização expressa. Os infratores respondem por perdas e danos. No caso do concessão de patentes de invenção, modelos de utilidade, modelos ou desenhos industriais, ficam reservados os direitos de exclusividade

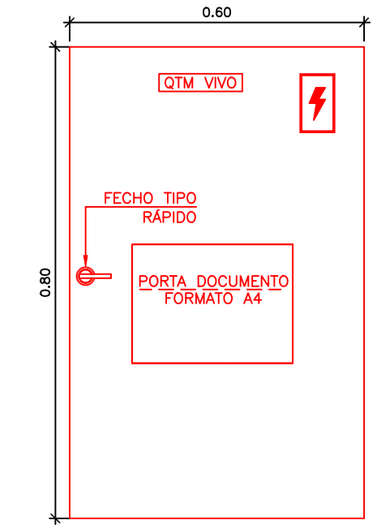


01 VISTA QUADRO FECHADO



02 DETALHE DA PLACA DE ADVERTÊNCIA

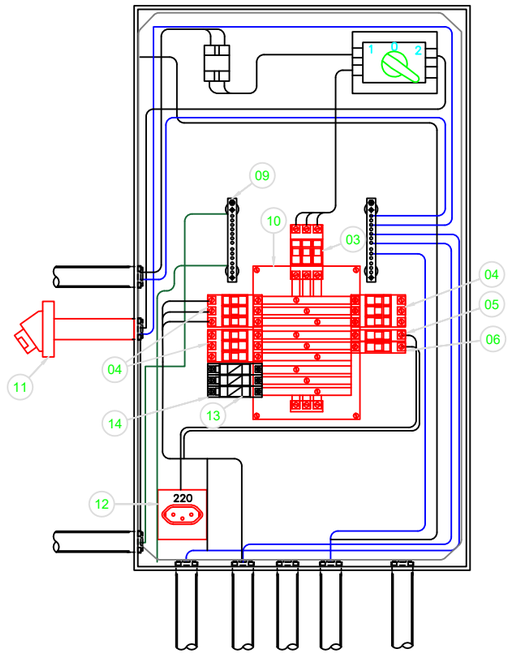

03 VISTA QUADRO ABERTO

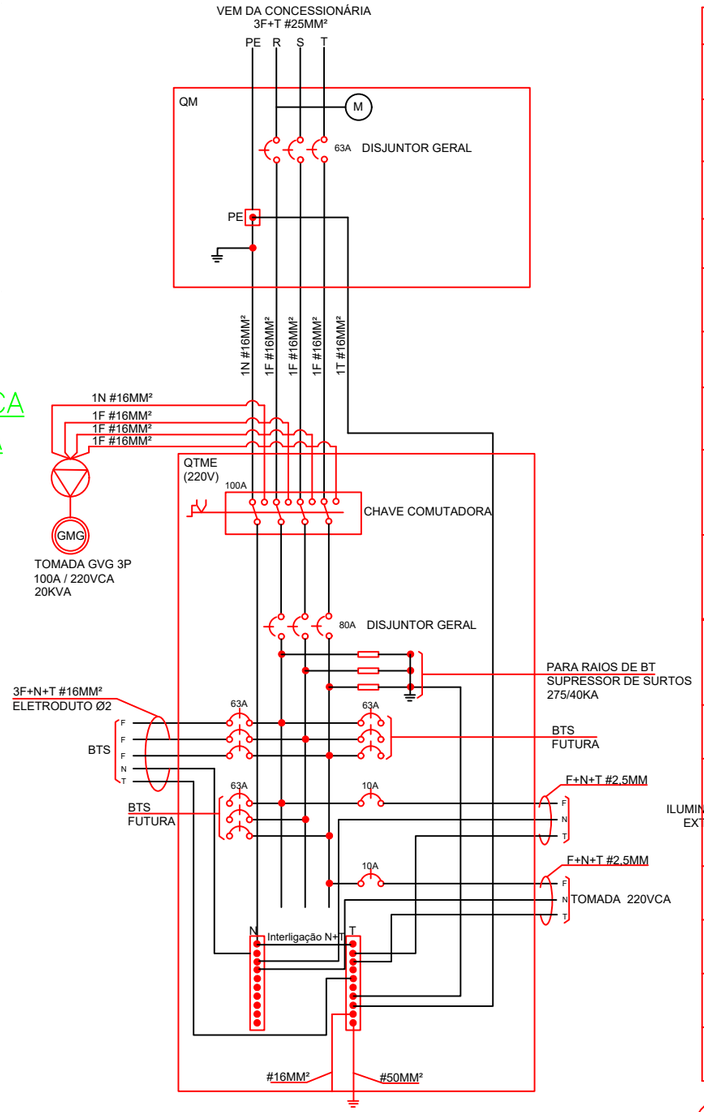

04 DIAGRAMA MULTIFILAR

LISTA DE MATERIAIS

ITEM	DESCRIÇÃO	QTD.
01	CAIXA METÁLICA (475X800X200MM) EM CHAAPA #14 1I 65, FECHADGURA COM CHAVE PADRÃO TIPO CENTRALIZADA COM TRAVA DUPLA	01
02	CHAVE COMUTADORA TRIPOLAR C/ MANOPLA IN-100A ICCF-31KA, TENSÃO 660V	01
03	DISJUNTOR TERMOMAGNÉTOCP TRIPOLAR 80A, ICC-5KA / 240VCA CONFORME NBR EX 60947-2	01
04	DISJUNTOR TERMOMAGNÉTOCP TRIPOLAR 63A, ICC-5KA / 240VCA CONFORME NBR EX 60947-2	03
05	DISJUNTOR TERMOMAGNÉTOCP MONOPOLAR 10A	01
06	DISJUNTOR TERMOMAGNÉTOCP MONOPOLAR 10A	01
07	BARRAMENTO DE COBRE ELETROLÍTICO PARA FASE DE ALTA CONDUTMDADE SEÇÃO RETANGULAR $\frac{1}{2}$"X $\frac{3}{16}$", SUPORTADOS POR ISOLADORES DE EPOXI OU RESINA POLIESTER	02
08	BARRAMENTO DE COBRE ELETROLÍTICO PARA NEUTRO DE ALTA CONDUTMDADE SEÇÃO RETANGULAR $\frac{1}{2}$"X $\frac{3}{16}$", SUPORTADOS POR ISOLADORES DE EPOXI OU RESINA POLIESTER	01
09	BARRAMENTO DE COBRE ELETROLÍTICO PARA TERRA DE ALTA CONDUTMDADE SEÇÃO RETANGULAR $\frac{1}{2}$"X $\frac{3}{16}$", SUPORTADOS POR ISOLADORES DE EPOXI OU RESINA POLIESTER	01
10	PLACA DE ACRÍLICO E=3MM PARA PROTEÇÃO DE BARRAMENTOS	01
11	TOMADA GMG 100A, STECK	01
12	TOMADA UNIVERSAL + TERRA 220V (F+N+T) MONTADA EM CONDULETE F" G" EMBUTIDO	01
13	PROTETOR DE SURTO SPW, CALSE I, IMAX - 25KA ONDA 8 / 20YS)	03
14	PONTE DE ATERRAMENTO PARA SUPRESSORES DE SURTO	01
15	PORTA DOCUMENTOS	01
16	ETIQUETA ACRÍLICA "QTM VIVO"	01

05 TABELA DE MATERIAIS

A entrega a terceiros e a reprodução deste documento, assim como o uso e a revelação do seu conteúdo, são proibidos, salvo por autorização expressa. Os infratores respondem por perdas e danos. No caso da concessão de patentes de invenção, modelos de utilidade, modelos ou desenhos industriais, ficam reservados os direitos de exclusividade

Pena	Esp.	Cor
1	0,15	7
2	0,25	7
3	0,20	7
4	0,15	7
5	0,40	7
6	0,50	7
7	0,20	7
8	0,15	7
9	0,10	7
10	0,15	1
20	0,15	1
30	0,20	7
80	0,15	3
98	0,20	98
142	0,15	142
170	0,15	5
210	0,15	6

ESCALA PLOT : 1/100
FORMATO ABNT A3 297x420


OBSERVAÇÕES:

COMENTÁRIO DE REVISÕES

REV.	DATA	DESCRIÇÃO	DESENHO	VERIFICAÇÃO
02	27/03/2026	COMPATIBILIZADO COM FUNDAÇÃO	FERA	WINITY
01	25/03/2026	ALTURA DAS ANTENAS	FERA	WINITY
00	16/03/2026	EMISSÃO INICIAL	FERA	WINITY

SOLICITANTE: vivo
CONCERSSIONÁRIA:
ENDEREÇO: POVOADO CANTINHO DO SENHOR DOS AFLITOS, N°27 - BARREIRAS/BA - CEP: 47.809-999
DETENTORA: winity TELECOM
COORDENADAS: LAT.: 11°59'52.59"S LONG.: 44°58'10.46"W
REVISÃO: 02
RESP. TÉC. EXECUÇÃO: F.E.R.A. PROJETOS E ENGENHARIA
PROJETO EXECUTIVO
SITE: BABRR002_C BACTI
EMISSÃO: 16/03/2026
ASSUNTO: DETALHE QTM
FOLHA: 11/15

FORMATO A3 (420x297mm)

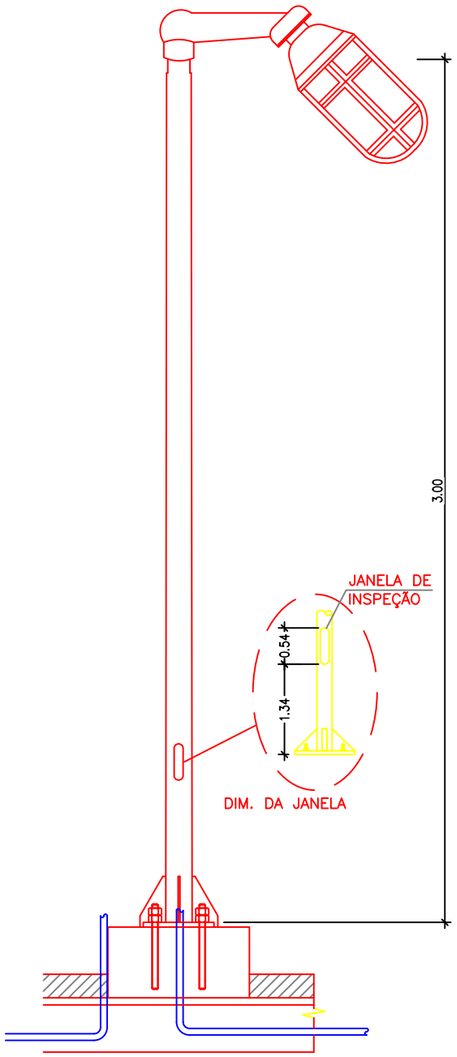

LEGENDA:


01 LUMINÁRIA TIPO ARANDELA

02 POSTE DE AÇO GALVANIZADO A FOGO Ø2.½"


03 ELETRODUTO DE PVC Ø1" PARA ENERGIA

04 ELETRODUTO DE PVC Ø1" PARA ATERRAMENTO

05 BASE DE CONCRETO 0,30x0,30x0,20m

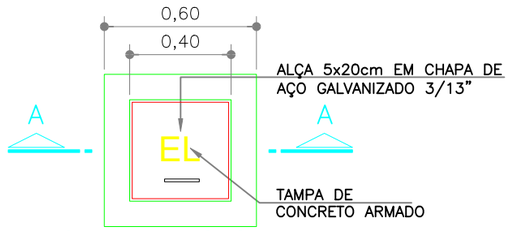


Planta Baixa (EL)
ESCALA 1:20

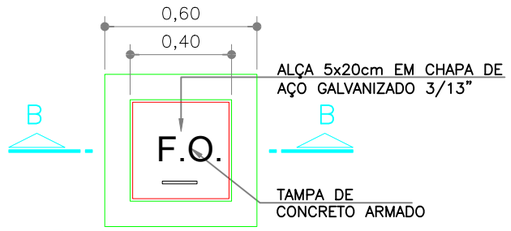


Planta Baixa (F.O)
ESCALA 1:20


DETALHE DO POÇO DE INSPEÇÃO
ESCALA 1:20

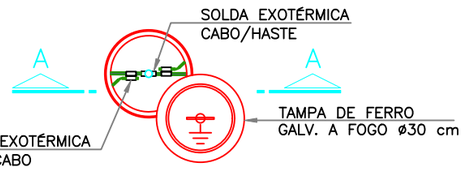


PLANTA
ESCALA 1:20

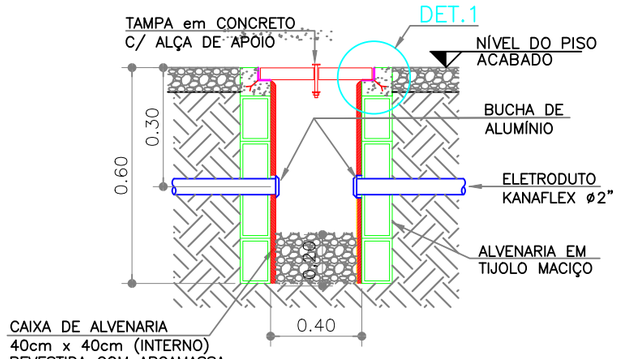


CORTE B-B
SEM ESCALA

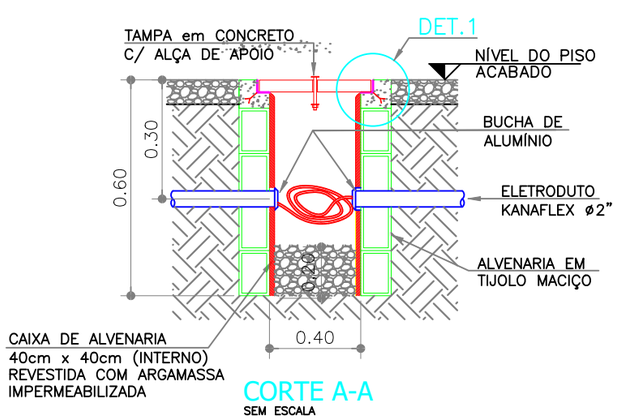


CORTE A-A
SEM ESCALA

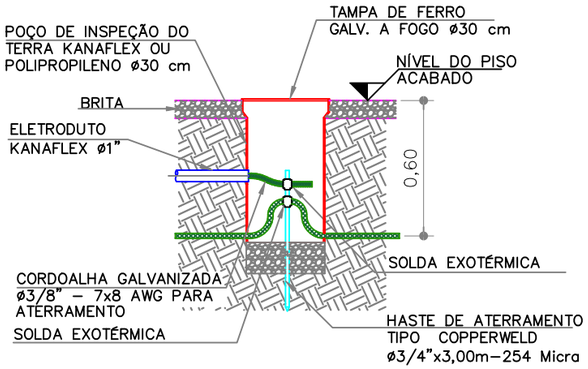

CORTE C-C
SEM ESCALA

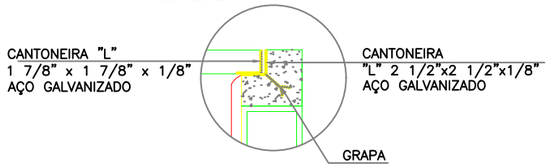


DETALHE-1
SEM ESCALA

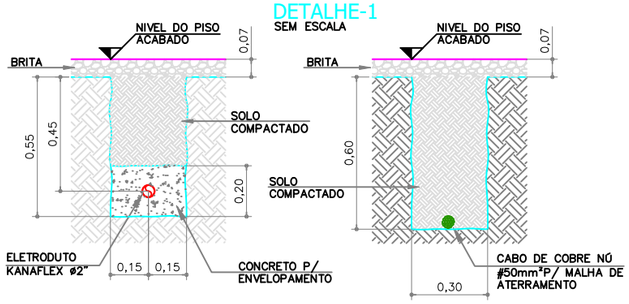

DETALHE DO ENVELOPAMENTO DAS TUBULAÇÕES
SEM ESCALA

DETALHE DA VALA DE ATERRAMENTO
SEM ESCALA

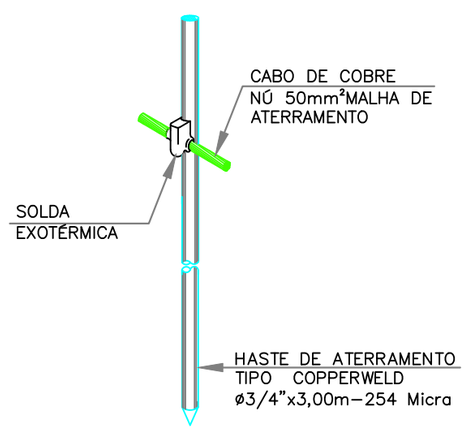

DET.HASTE DE ATERRAMENTO
SEM ESCALA

NOTAS:

01 – NAS CAIXAS DE PASSAGEM OS ELETRODUTOS DE KANAFLEX DEVERÃO ESTAR COM ACABAMENTO EM BUCHA DE ALUMINIO, EVITANDO ARRANHAR OU DANIFICAR A ISOLAÇÃO DOS CABOS. OS ELETRODUTOS DEVERÃO TAMBÉM SER VEDADOS COM " ESPUMA DE POLIURETANO"

02 – TODOS OS CABOS DEVERÃO SER IDENTIFICADOS COM ANILHA CONTENDO O NOME DA OPERADORA

03 – TODAS AS PEÇAS METALICAS DEVERÃO SER GALVANIZADAS A FOGO

04 – A CONSTRUTORA DEVERA DEIXAR UM ARAME GUIA GALVANIZADO NA TUBULAÇÃO DE ELÉTRICA

05 – TODAS AS TAMPAS DAS CAIXAS DE PASSAGEM DEVEM TER IDENTIFICAÇÃO EM BAIXO RELEVO, COM AS SEGUINTES SIGLAS: FO – FIBRA OPTICA / EL – ELÉTRICA / AT – ATERRAMENTO

06 – AS TAMPAS DAS CAIXAS DE PASSAGEM DE CABOS E INSPEÇÃO DEVERAM SER PINTADAS COM TINTA "NOVA COR" NA COR CONCRETO.

07 – APÓS A PASSAGEM DOS CABOS DE ENERGIA E ATERRAMENTO AS CAIXAS DE PASSAGEM DE ELÉTRICA E ATERRAMENTO DEVERAM SER PREENCHIDAS COM BRITA E AS TAMPAS SOLDADAS NOS QUATRO CANTOS.

A entrega e terceiros e a reprodução deste documento, assim como o uso e a revelação do seu conteúdo, são proibidos, salvo por autorização expressa. Os infratores respondem por perdas e danos. No caso da concessão de patentes de invenção, modelos de utilidade, modelos ou desenhos industriais, ficam reservados os direitos de exclusividade

Pena	Esp.	Cor
1	0,15	7
2	0,25	7
3	0,20	7
4	0,15	7
5	0,40	7
6	0,50	7
7	0,20	7
8	0,15	7
9	0,10	7
10	0,15	1
20	0,15	1
30	0,20	7
80	0,15	3
98	0,20	98
142	0,15	142
170	0,15	5
210	0,15	6

ESCALA PLOT : 1/100
FORMATO ABNT A3 297x420

FORMATO A3 (420x297mm)

OBSERVAÇÕES:

COMENTÁRIO DE REVISÕES

REV.	DATA	DESCRIÇÃO	DESENHO	VERIFICAÇÃO
02	27/03/2026	COMPATIBILIZADO COM FUNDAÇÃO	FERA	WINITY
01	25/03/2026	ALTURA DAS ANTENAS	FERA	WINITY
00	16/03/2026	EMISSÃO INICIAL	FERA	WINITY

SOLICITANTE: vivo

CONCERSSIONÁRIA:

ENDEREÇO: **POVOADO CANTINHO DO SENHOR DOS AFLITOS, N°27 - BARREIRAS/BA - CEP: 47.809-999**

DETENTORA: winity TELECOM

COORDENADAS: **LAT.: 11°59'52.59"S LONG.: 44°58'10.46"W**

REVISÃO: 02

RESP. TÉC. EXECUÇÃO: F.E.R.A. PROJETOS E ENGENHARIA


PROJETO EXECUTIVO

SITE: BABRR002_C BACTI


EMISSÃO: 16/03/2026

ASSUNTO: CAIXAS DE PASSAGEM


FOLHA: 12/15

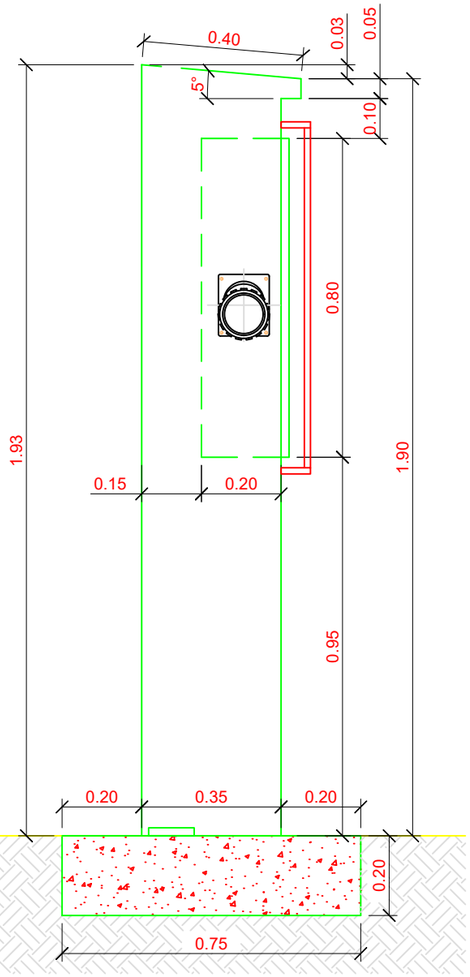

CORTE A
SEM ESCALA

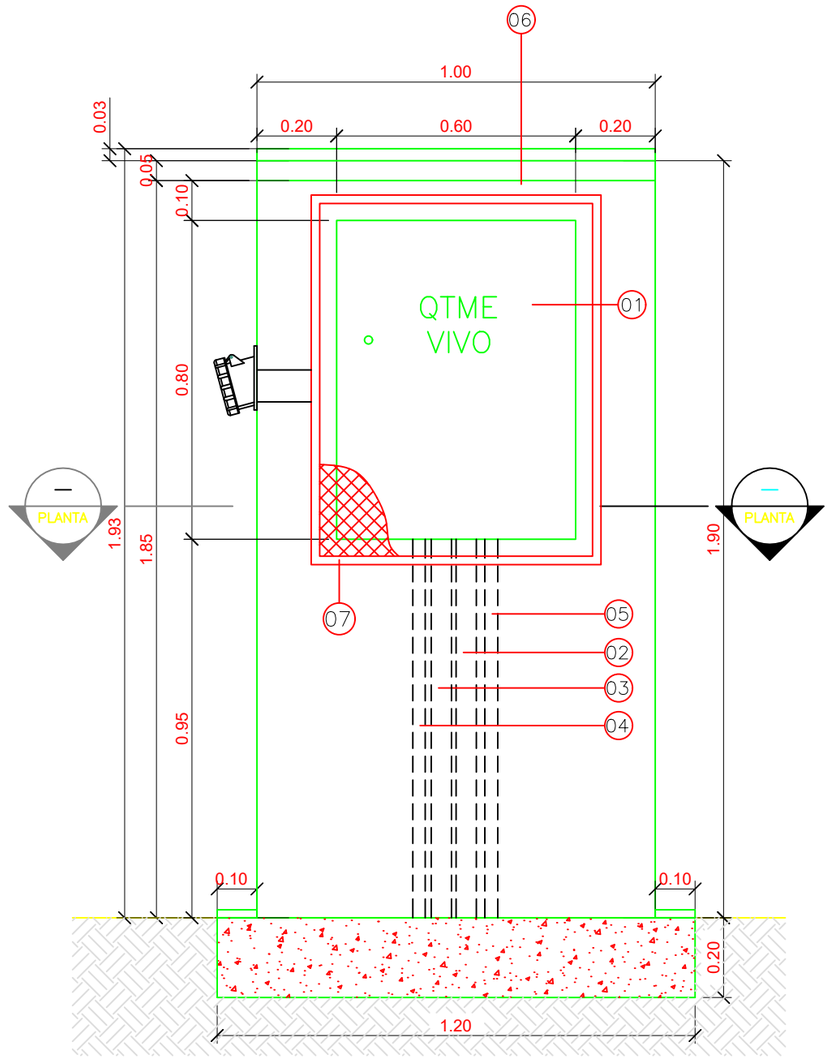

CORTE B
SEM ESCALA

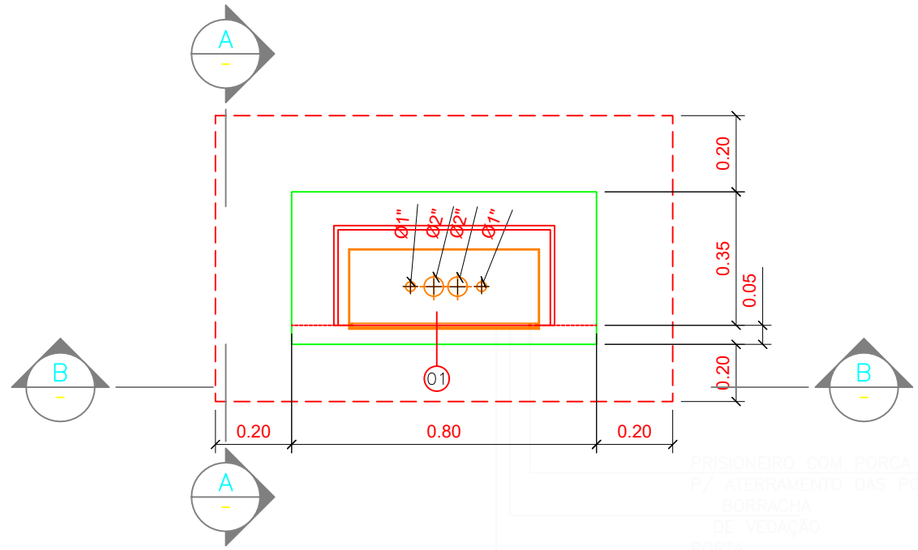

PLANTA DO QTM
SEM ESCALA

LEGENDAS:

1. QTME VIVO A INSTALAR;
2. ELETRODUTO DE KANAFLEX RÍGIDO ø2" + CABOS DE ENERGIA (3F+N+T) #16mm²–0,6/1kV–KANAFLEX–FLEXÍVEL, (VAI DO MEDIDOR ATÉ O QTME) VIVO A INSTALAR;
3. ELETRODUTO DE KANAFLEX RÍGIDO ø2" + CABOS DE ENERGIA (3F+N+T) #16mm²–0,6/1kV–KANAFLEX FLEXÍVEL, (VAI DO QTME ATÉ O BASTIDOR 1) VIVO A INSTALAR;
4. ELETRODUTO DE KANAFLEX RÍGIDO ø1" + CABOS DE ENERGIA (F+N) #2,5mm²–0,6/1kV–KANAFLEX FLEXÍVEL, (VAI DO QTME ATÉ A LUMINÁRIA) VIVO A INSTALAR;
5. ELÉTRODUTO KANAFLEX RÍGIDO ø1" PARA CABO DE ATERRAMENTO 1#50mm² 0,6/1KV VERDE ISOLADO;
6. ABRIGO EM ALVENARIA COM PINGADEIRA.
7. GRADIL PARA PROTEÇÃO DO QTME COM CADEADO CR50 A INSTALAR.

A entrega a terceiros e a reprodução deste documento, assim como o uso e a revelação do seu conteúdo, são proibidos, salvo por autorização expressa. Os infratores respondem por perdas e danos. No caso da concessão de patentes de invenção, modelos de utilidade, modelos ou desenhos industriais, ficam reservados os direitos de exclusividade

Pena	Esp.	Cor
1	0,15	7
2	0,25	7
3	0,20	7
4	0,15	7
5	0,40	7
6	0,50	7
7	0,20	7
8	0,15	7
9	0,10	7
10	0,15	1
20	0,15	1
30	0,20	7
80	0,15	3
98	0,20	98
142	0,15	142
170	0,15	5
210	0,15	6

ESCALA PLOT : 1/100
FORMATO ABNT A3 297x420

FORMATO A3 (420x297mm)

OBSERVAÇÕES:

COMENTÁRIO DE REVISÕES

REV.	DATA	DESCRIÇÃO	DESENHO	VERIFICAÇÃO
02	27/03/2026	COMPATIBILIZADO COM FUNDAÇÃO	FERA	WINITY
01	25/03/2026	ALTURA DAS ANTENAS	FERA	WINITY
00	16/03/2026	EMISSÃO INICIAL	FERA	WINITY

SOLICITANTE: vivo
CONCERSSIONÁRIA:
ENDEREÇO: POVOADO CANTINHO DO SENHOR DOS AFLITOS, N°27 - BARREIRAS/BA - CEP: 47.809-999
DETENTORA: winity TELECOM
COORDENADAS: LAT.: 11°59'52.59"S LONG.: 44°58'10.46"W
REVISÃO: 02
RESP. TÉC. EXECUÇÃO: F.E.R.A. PROJETOS E ENGENHARIA
PROJETO EXECUTIVO
SITE: BABRR002_C BACTI
EMISSÃO: 16/03/2026
ASSUNTO: ABRIGO QTM/QTM
FOLHA: 13/15

A:

E AÇO FORMAÇÃO 7 FIOS 3/8", CLASSE DE GALVANIZAÇÃO
RGA DE RUPTURA S.M. - ATERRAMENTO EXPOSTO AO

E AÇO FORMAÇÃO 7 FIOS 3/8", CLASSE DE GALVANIZAÇÃO
RGA DE RUPTURA S.M. - ATERRAMENTO ALAMBRADO

E COBRE NU #50mm², TÊMPERA MEIO DURA, ENTERRADO A
MO 30,0cm (ATERRAMENTO DA FERRAGEM DO
MENTO)

E AÇO #50mm² ATERRAMENTO MEDIÇÃO

E COBRE VERDE ISOLADO #50mm² ATERRAMENTO
MENTOS - DEIXAR FOLGA 1,5m ACIMA DA BASE PROTEGIDO
ALTUBE

E ATERRAMENTO DE SEÇÃO CIRCULAR Ø5/8" EM AÇO
ZADO COM ALTA CAMADA DE COBRE (254 um) h=3,0m

XOTÉRMICA TIPO CABO-HASTE

XOTÉRMICA CABO-CABO

LHA DE COBRE NÚ ESTANHADO FLEXÍVEL 1" COM
ORES PARA FIXAÇÃO

COBRE NU #50mm², TÊMPERA MEIO DURA, ENTERRADO A
MO 60,0cm
ALHE 4

AÇO FORMAÇÃO 7 FIOS 3/8", CLASSE DE GALVANIZAÇÃO
RGA DE RUPTURA S.M. - ATERRAMENTO TGB

COBRE VERDE ISOLADO #50mm² - ATERRAMENTO QDE

OLOGIA:

ABO DE AÇO Ø3/8"
ABO DE COBRE NU
ABO DE COBRE VERDE, ISOLAÇÃO 0,6/1kV
ASTE DE ATERRAMENTO COPPERWELD 3/4"x3,00m
ONECTOR FCI
ERMINAL PRESSÃO OU CONECTOR SPLITBOLT
ARRA DE ATERRAMENTO

VAÇÕES:

ES:
DE ATERRAMENTO DEVERÁ SER EXECUTADA CONFORME NORMA
M RESISTIVIDADE MENOR QUE 10OHMS;

S PONTOS DE ATERRAMENTO DA MALHA DEVEM SER INTERLIGADOS

S DA MALHA DE ATERRAMENTO DEVEM SER INSTALADO A UMA
ADE MÍNIMA DE 50cm DA SUPERFÍCIE;


RAMENTOS DAS PARTES METÁLICAS APARENTES (ALAMBRADO,
BASE DO POSTE) DEVERÃO SER REALIZADOS COM CABO DE AÇO
GADOS COM CONECTOR BIMETÁLICO;

AMENTO DO QTM E GABINETES DEVERÃO SER REALIZADOS COM
E # 16mm²;


AMENTO DO ALAMBRADO DEVERÁ SER REALIZADO COM CABO DE
ERLIGADO COM SPLITBOLT ATÉ A CONCERTINA;

ES DE ATERRAMENTO TIPO COPPERWELD 3/4" x 3.00m DEVERÃO SER
A UMA DISTÂNCIA MINIMA DE 3,00m E DE NO MÁXIMO 5,00m;


ATERRAMENTO DAS FUNDAÇÕES, DEVERÁ SEGUIR A SEGUINTE
O:
NDAÇÕES DO TIPO TUBULÃO, DEVERÁ SER INSTALADA UMA HASTE
AO FUNDO DO MESMO COM CABO DE COBRE NÚ # 50mm²
OS À ARMADURA DA FUNDAÇÃO;
NDAÇÕES DO TIPO RADIER, A MALHA DE ATERRAMENTO DO SITE
R INTERLIGADA À SUA ARMADURA COM CABO DE COBRE NU;
NDAÇÕES DO TIPO ESTACA, A MALHA DE ATERRAMENTO DO SITE
R INTERLIGADA À SUA ARMADURA COM CABO DE COBRE NU.

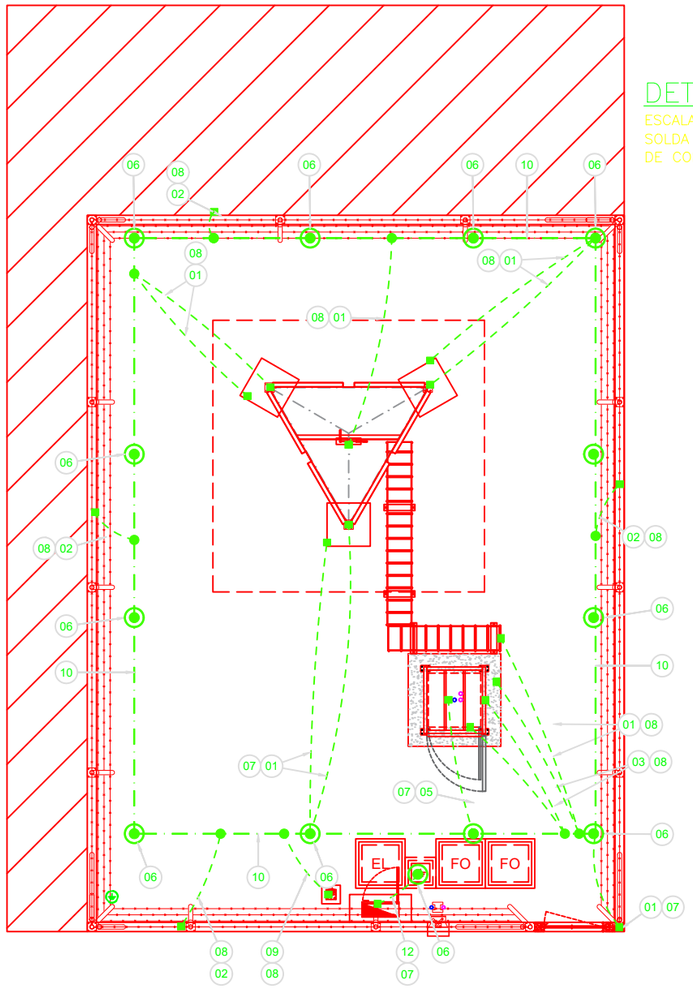


01 PLANTA BAIXA
1:100

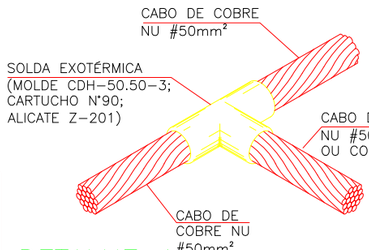

DETALHE 1
ESCALA: SEM ESCALA
SOLDA EXOTÉRMICA ENTRE CABOS
DE COBRE #50mm2

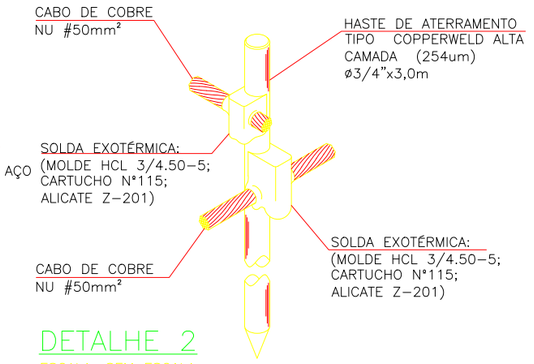

DETALHE 2
ESCALA: SEM ESCALA
SOLDA EXOTÉRMICA ENTRE CABOS
DE COBRE #50mm2 E HASTE ø3/4"

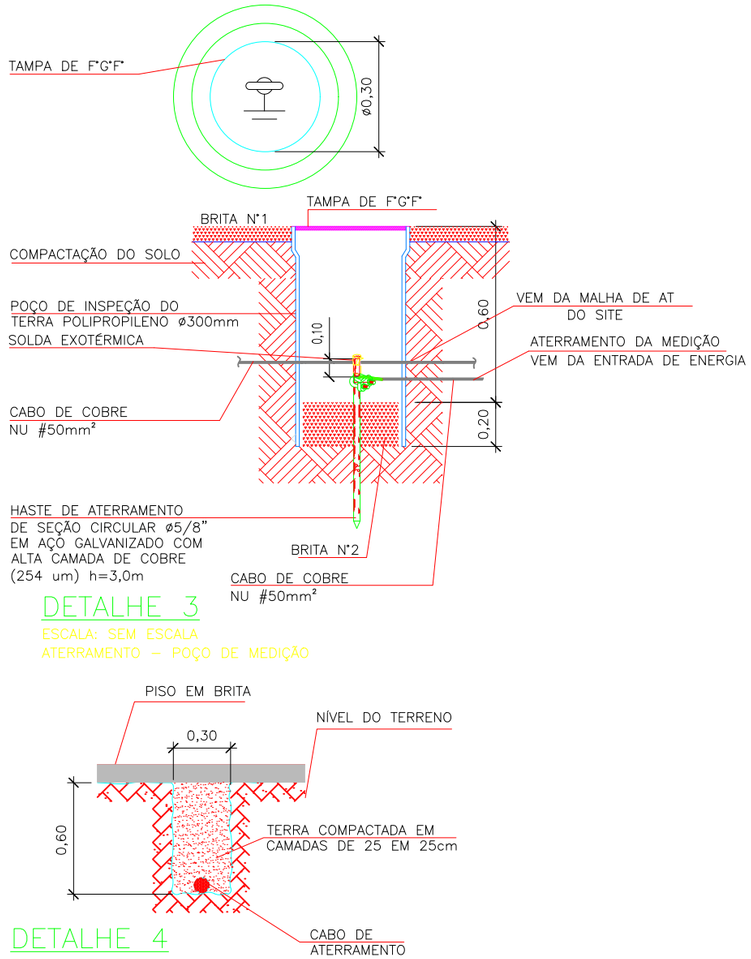

DETALHE 3
ESCALA: SEM ESCALA
ATERRAMENTO – POÇO DE MEDIÇÃO

DETALHE 4
ESCALA: SEM ESCALA
IMPLANTAÇÃO DO CABO DE
ATERRAMENTO

Pena	Esp.	Cor
1	0,15	7
2	0,25	7
3	0,20	7
4	0,15	7
5	0,40	7
6	0,50	7
7	0,20	7
8	0,15	7
9	0,10	7
10	0,15	1
20	0,15	1
30	0,20	7
80	0,15	3
98	0,20	98
142	0,15	142
170	0,15	5
210	0,15	6

ESCALA PLOT : 1/100
FORMATO ABNT A3 297x420

OBSERVAÇÕES:


COMENTÁRIO DE REVISÕES


REV.	DATA	DESCRIÇÃO	DESENHO	VERIFICAÇÃO
02	27/03/2026	COMPATIBILIZADO COM FUNDAÇÃO	FERA	WINITY
01	25/03/2026	ALTURA DAS ANTENAS	FERA	WINITY
00	16/03/2026	EMISSÃO INICIAL	FERA	WINITY


SOLICITANTE: vivo
CONCERSSIONÁRIA:
ENDEREÇO: POVOADO CANTINHO DO SENHOR DOS AFLITOS, N°27 - BARREIRAS/BA - CEP: 47.809-999
DETENTORA: winity TELECOM
COORDENADAS: LAT.: 11°59'52.59"S LONG.: 44°58'10.46"W
REVISÃO: 02
RESP. TÉC. EXECUÇÃO: F.E.R.A. PROJETOS E ENGENHARIA
PROJETO EXECUTIVO
SITE: BABRR002_C BACTI
EMISSÃO: 16/03/2026
ASSUNTO: PLANTA ATERRAMENTO
FOLHA: 14/15


FORMATO A3 (420x297mm)

A entrega a terceiros e a reprodução deste documento, assim como o uso e a revelação do seu conteúdo, são proibidos, salvo por autorização expressa. Os infratores respondem por perdas e danos. No caso da concessão de patentes de invenção, modelos de utilidade, modelos ou desenhos industriais, ficam reservados os direitos de exclusividade

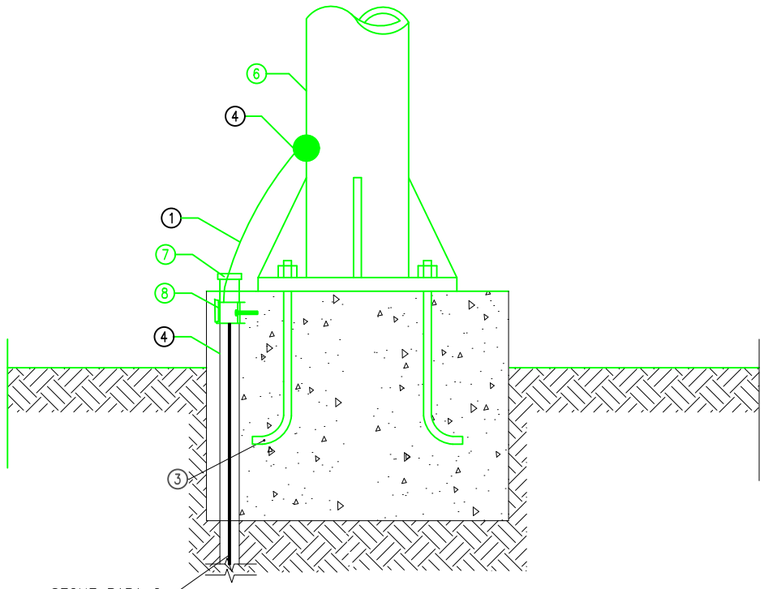


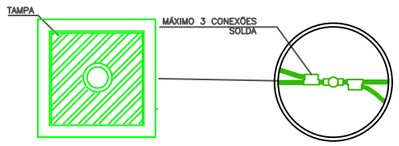

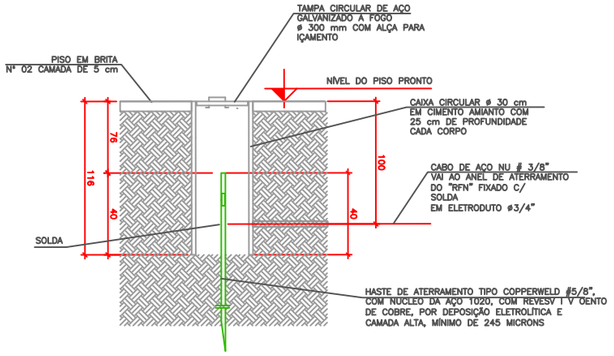


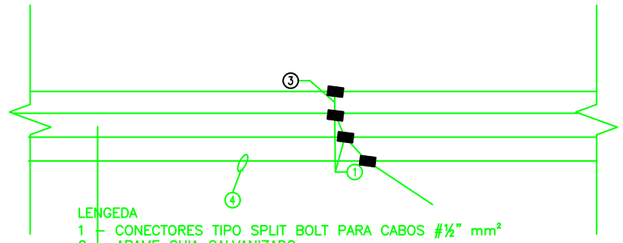


LENGEDA
1 – CONECTORES TIPO SPLIT BOLT PARA CABOS #½" mm²
2 – ARAME GUIA GALVANIZADO
3 – CABO DE AÇO GALVANIZADO 3/8"
4 – ARAME FARPADO

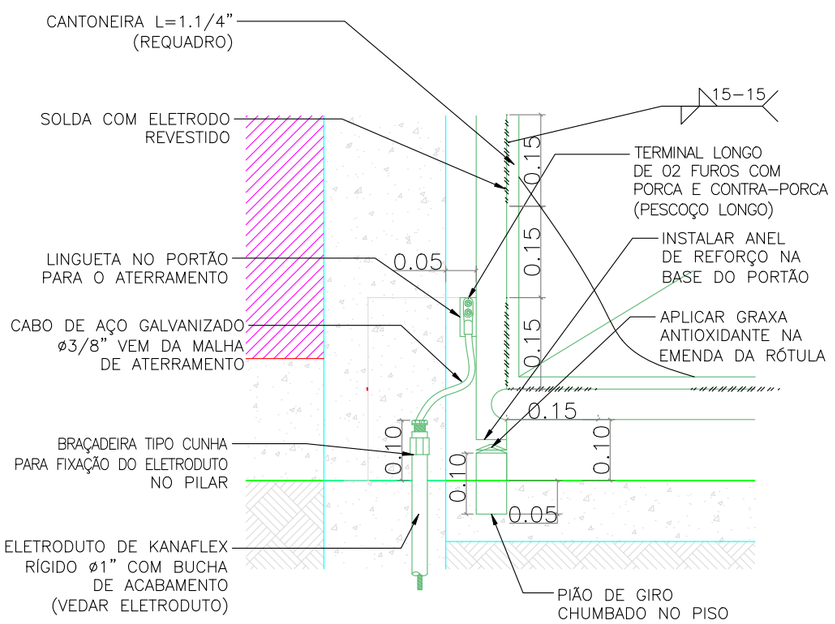


DETALHE D

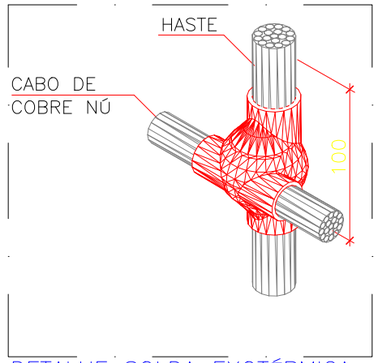

DETALHE SOLDA EXOTÉRMICA CABOxHASTE
SEM ESCALA

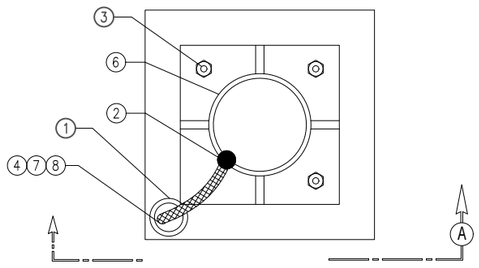

LENGEDA
1 – CABO DE AÇO 3/8"
2 – SPLIT BOLT C/ RABICHO
3 – CHUMBADORES
4 – TUBO DE KANAFLEX ø1"
5 – CONECTOR SOLDA EXOTÉRMICA – CABOxCABO
6 – ESTRUTURA
7 – BUCHA DE ALUMÍNIO
8 – ABRAÇADEIRA TIPO CUNHA

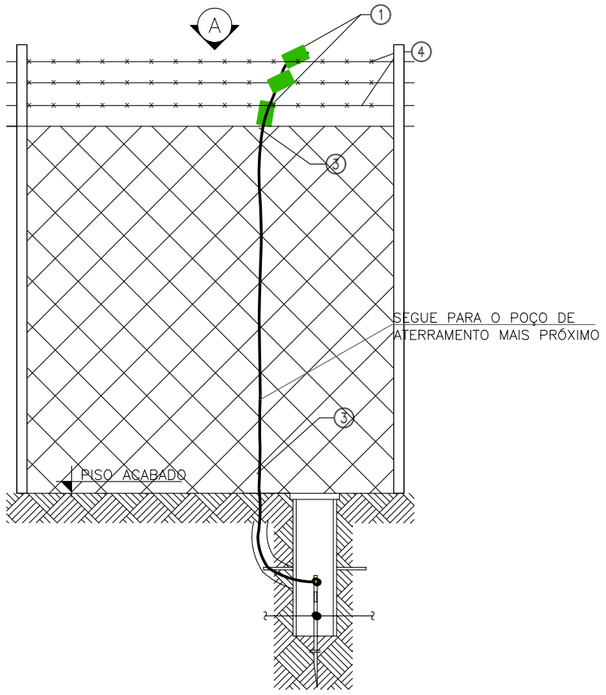

Pena	Esp.	Cor
1	0,15	7
2	0,25	7
3	0,20	7
4	0,15	7
5	0,40	7
6	0,50	7
7	0,20	7
8	0,15	7
9	0,10	7
10	0,15	1
20	0,15	1
30	0,20	7
80	0,15	3
98	0,20	98
142	0,15	142
170	0,15	5
210	0,15	6

ESCALA PLOT : 1/100
FORMATO ABNT A3 297x420

FORMATO A3 (420x297mm)

A entrega a terceiros e a reprodução deste documento, assim como o uso e a revelação do seu conteúdo, são proibidos, salvo por autorização expressa. Os infratores respondem por perdas e danos. No caso do concessão de patentes de invenção, modelos de utilidade, modelos ou desenhos industriais, ficam reservados os direitos de exclusividade.

OBSERVAÇÕES:

COMENTÁRIO DE REVISÕES

REV.	DATA	DESCRIÇÃO	DESENHO	VERIFICAÇÃO
02	27/03/2026	COMPATIBILIZADO COM FUNDAÇÃO	FERA	WINITY
01	25/03/2026	ALTURA DAS ANTENAS	FERA	WINITY
00	16/03/2026	EMISSÃO INICIAL	FERA	WINITY

SOLICITANTE: vivo

CONCERSSIONÁRIA:

ENDEREÇO: **POVOADO CANTINHO DO SENHOR DOS AFLITOS, N°27 - BARREIRAS/BA - CEP: 47.809-999**

DETENTORA: winity TELECOM

COORDENADAS: **LAT.: 11°59'52.59"S LONG.: 44°58'10.46"W**

REVISÃO: 02

RESP. TÉC. EXECUÇÃO: F.E.R.A. PROJETOS E ENGENHARIA

PROJETO EXECUTIVO

SITE: BABRR002_C BACTI

EMISSÃO: 16/03/2026

ASSUNTO: DETALHES ATERRAMENTO

FOLHA: 15/15